


1 2 3



LAKE COUNTRY
CONSTRUCTION GROUP

General Contractor: Lake Country Construction Group
161 Horizon Dr. | Verona, WI 53593
608.845.1398

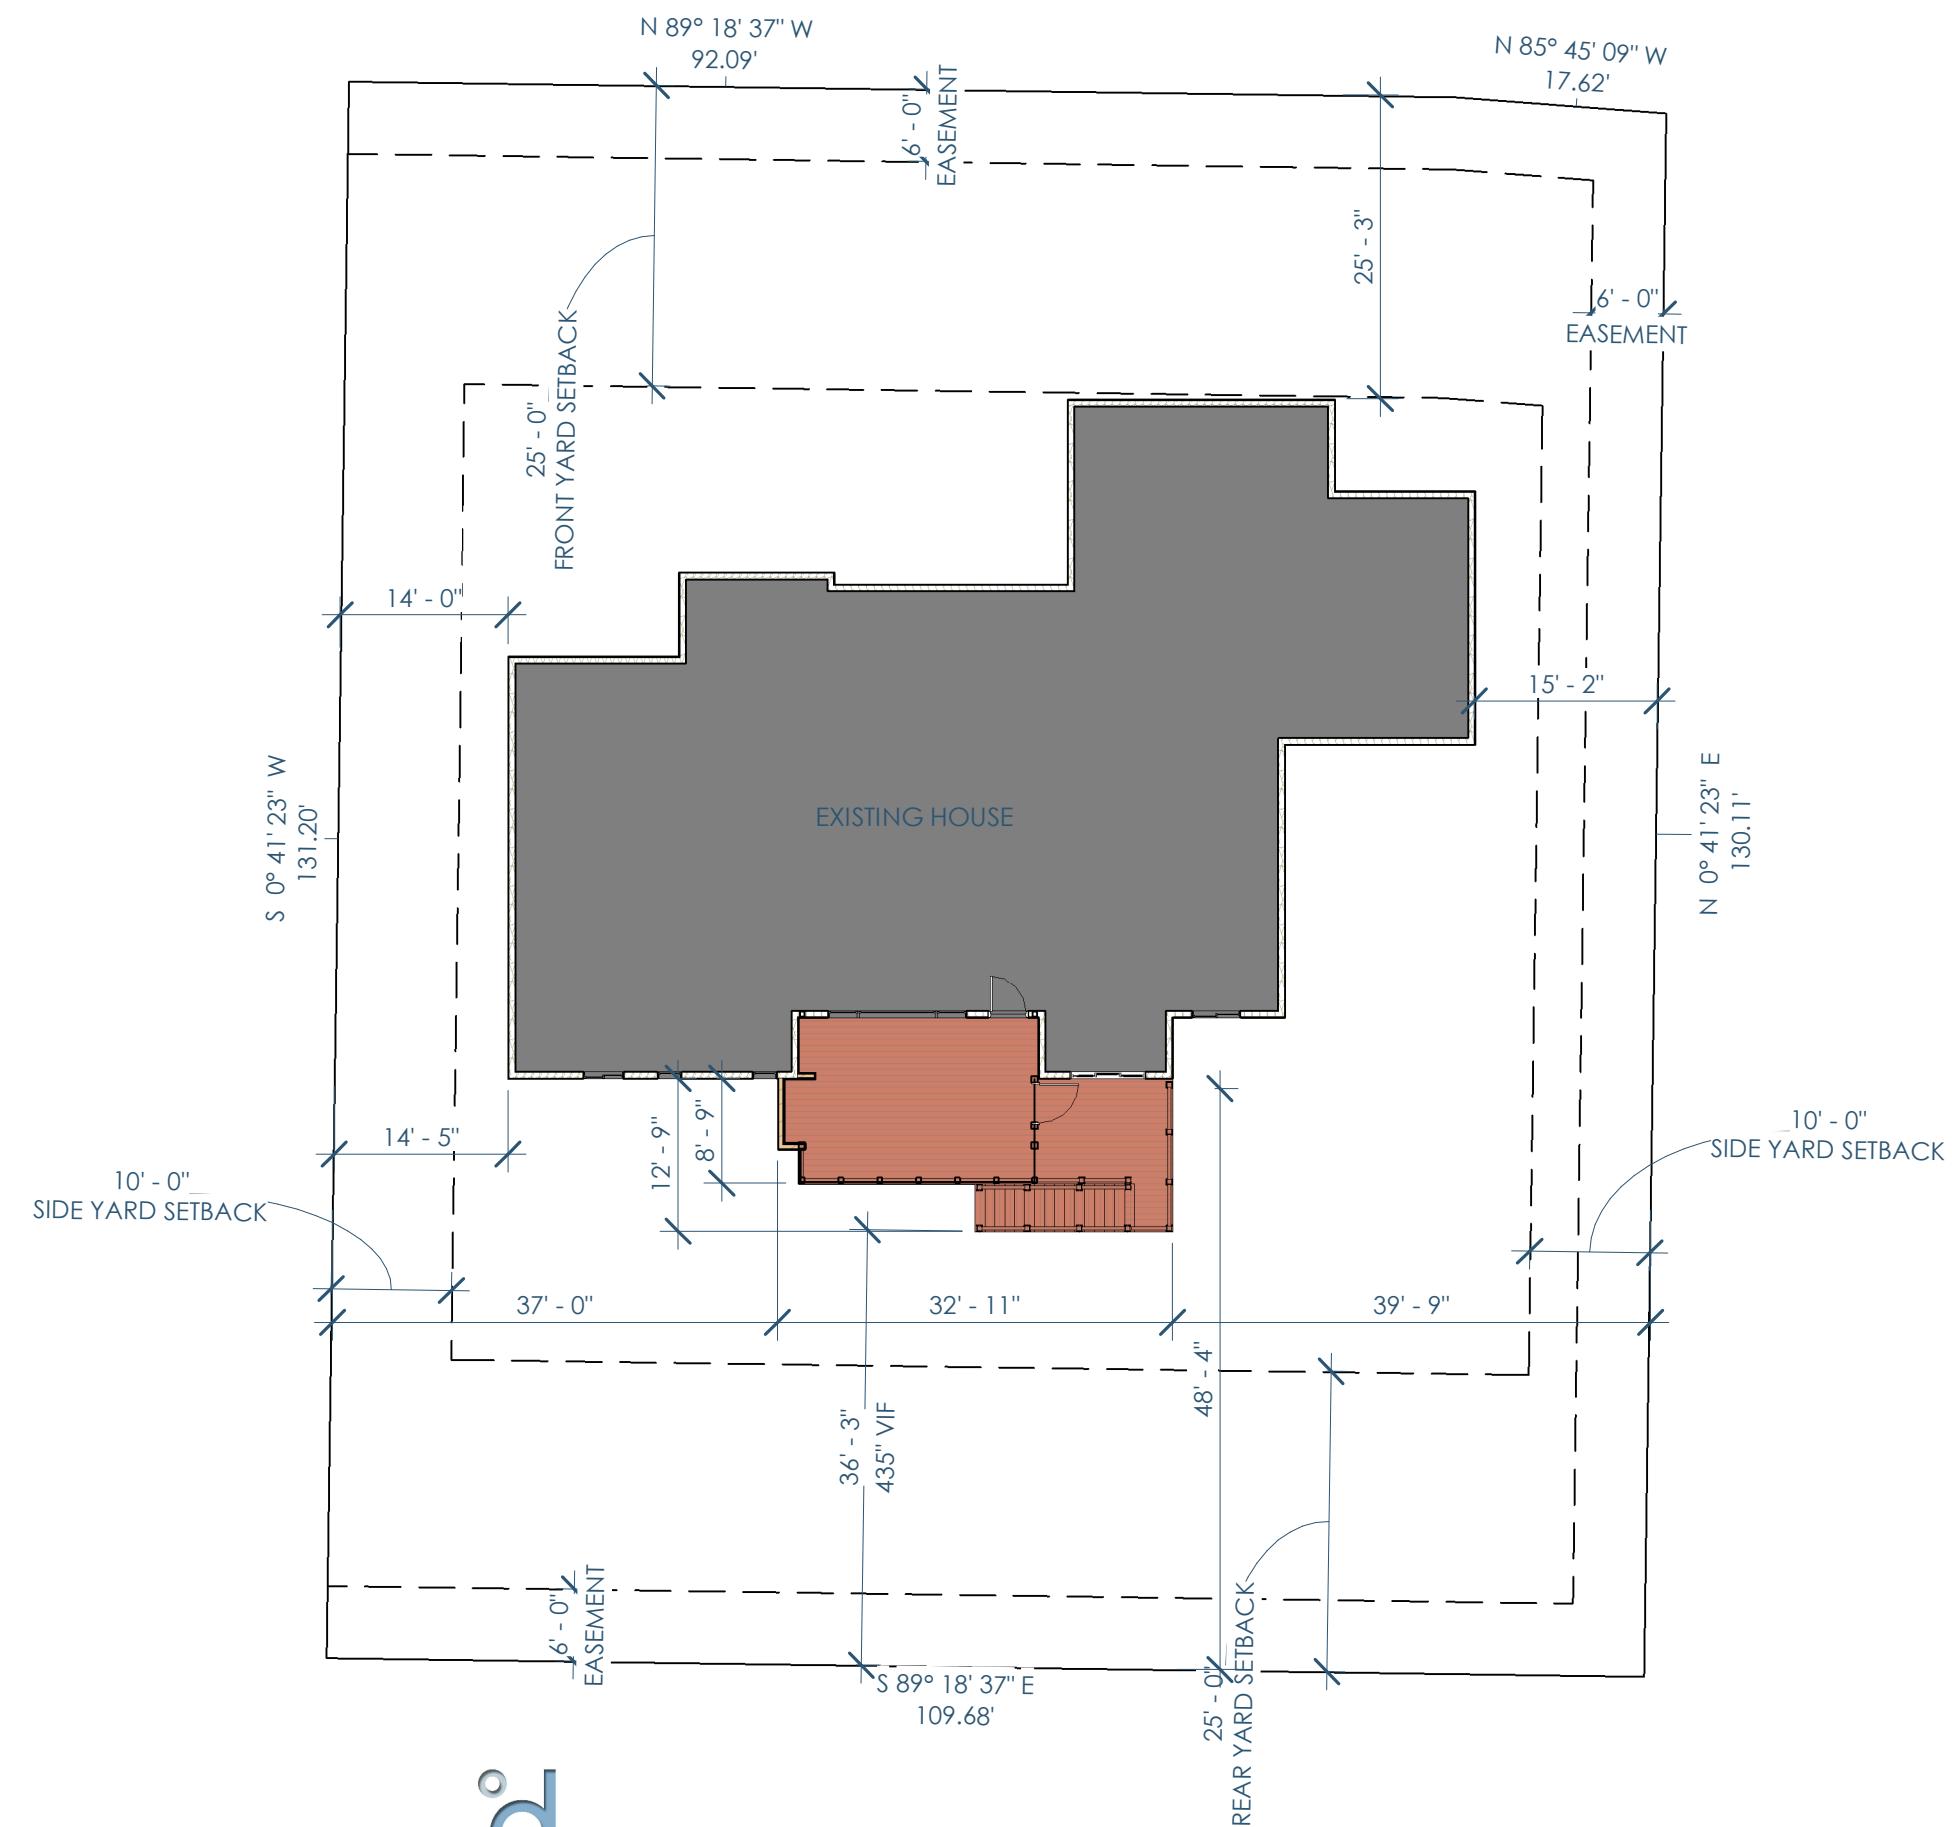

Architect: OpeningDesign


316 W Washington Ave. | Suite 675 | Madison, WI 53703
ryan@openingdesign.com | 773.425.6456

HERNAN RESIDENCE - 05.29.2018
453 MATTERHORN DR - VERONA WI 53593
SITE PLAN - (A050)



0 8' 16' 32'

1 2 3

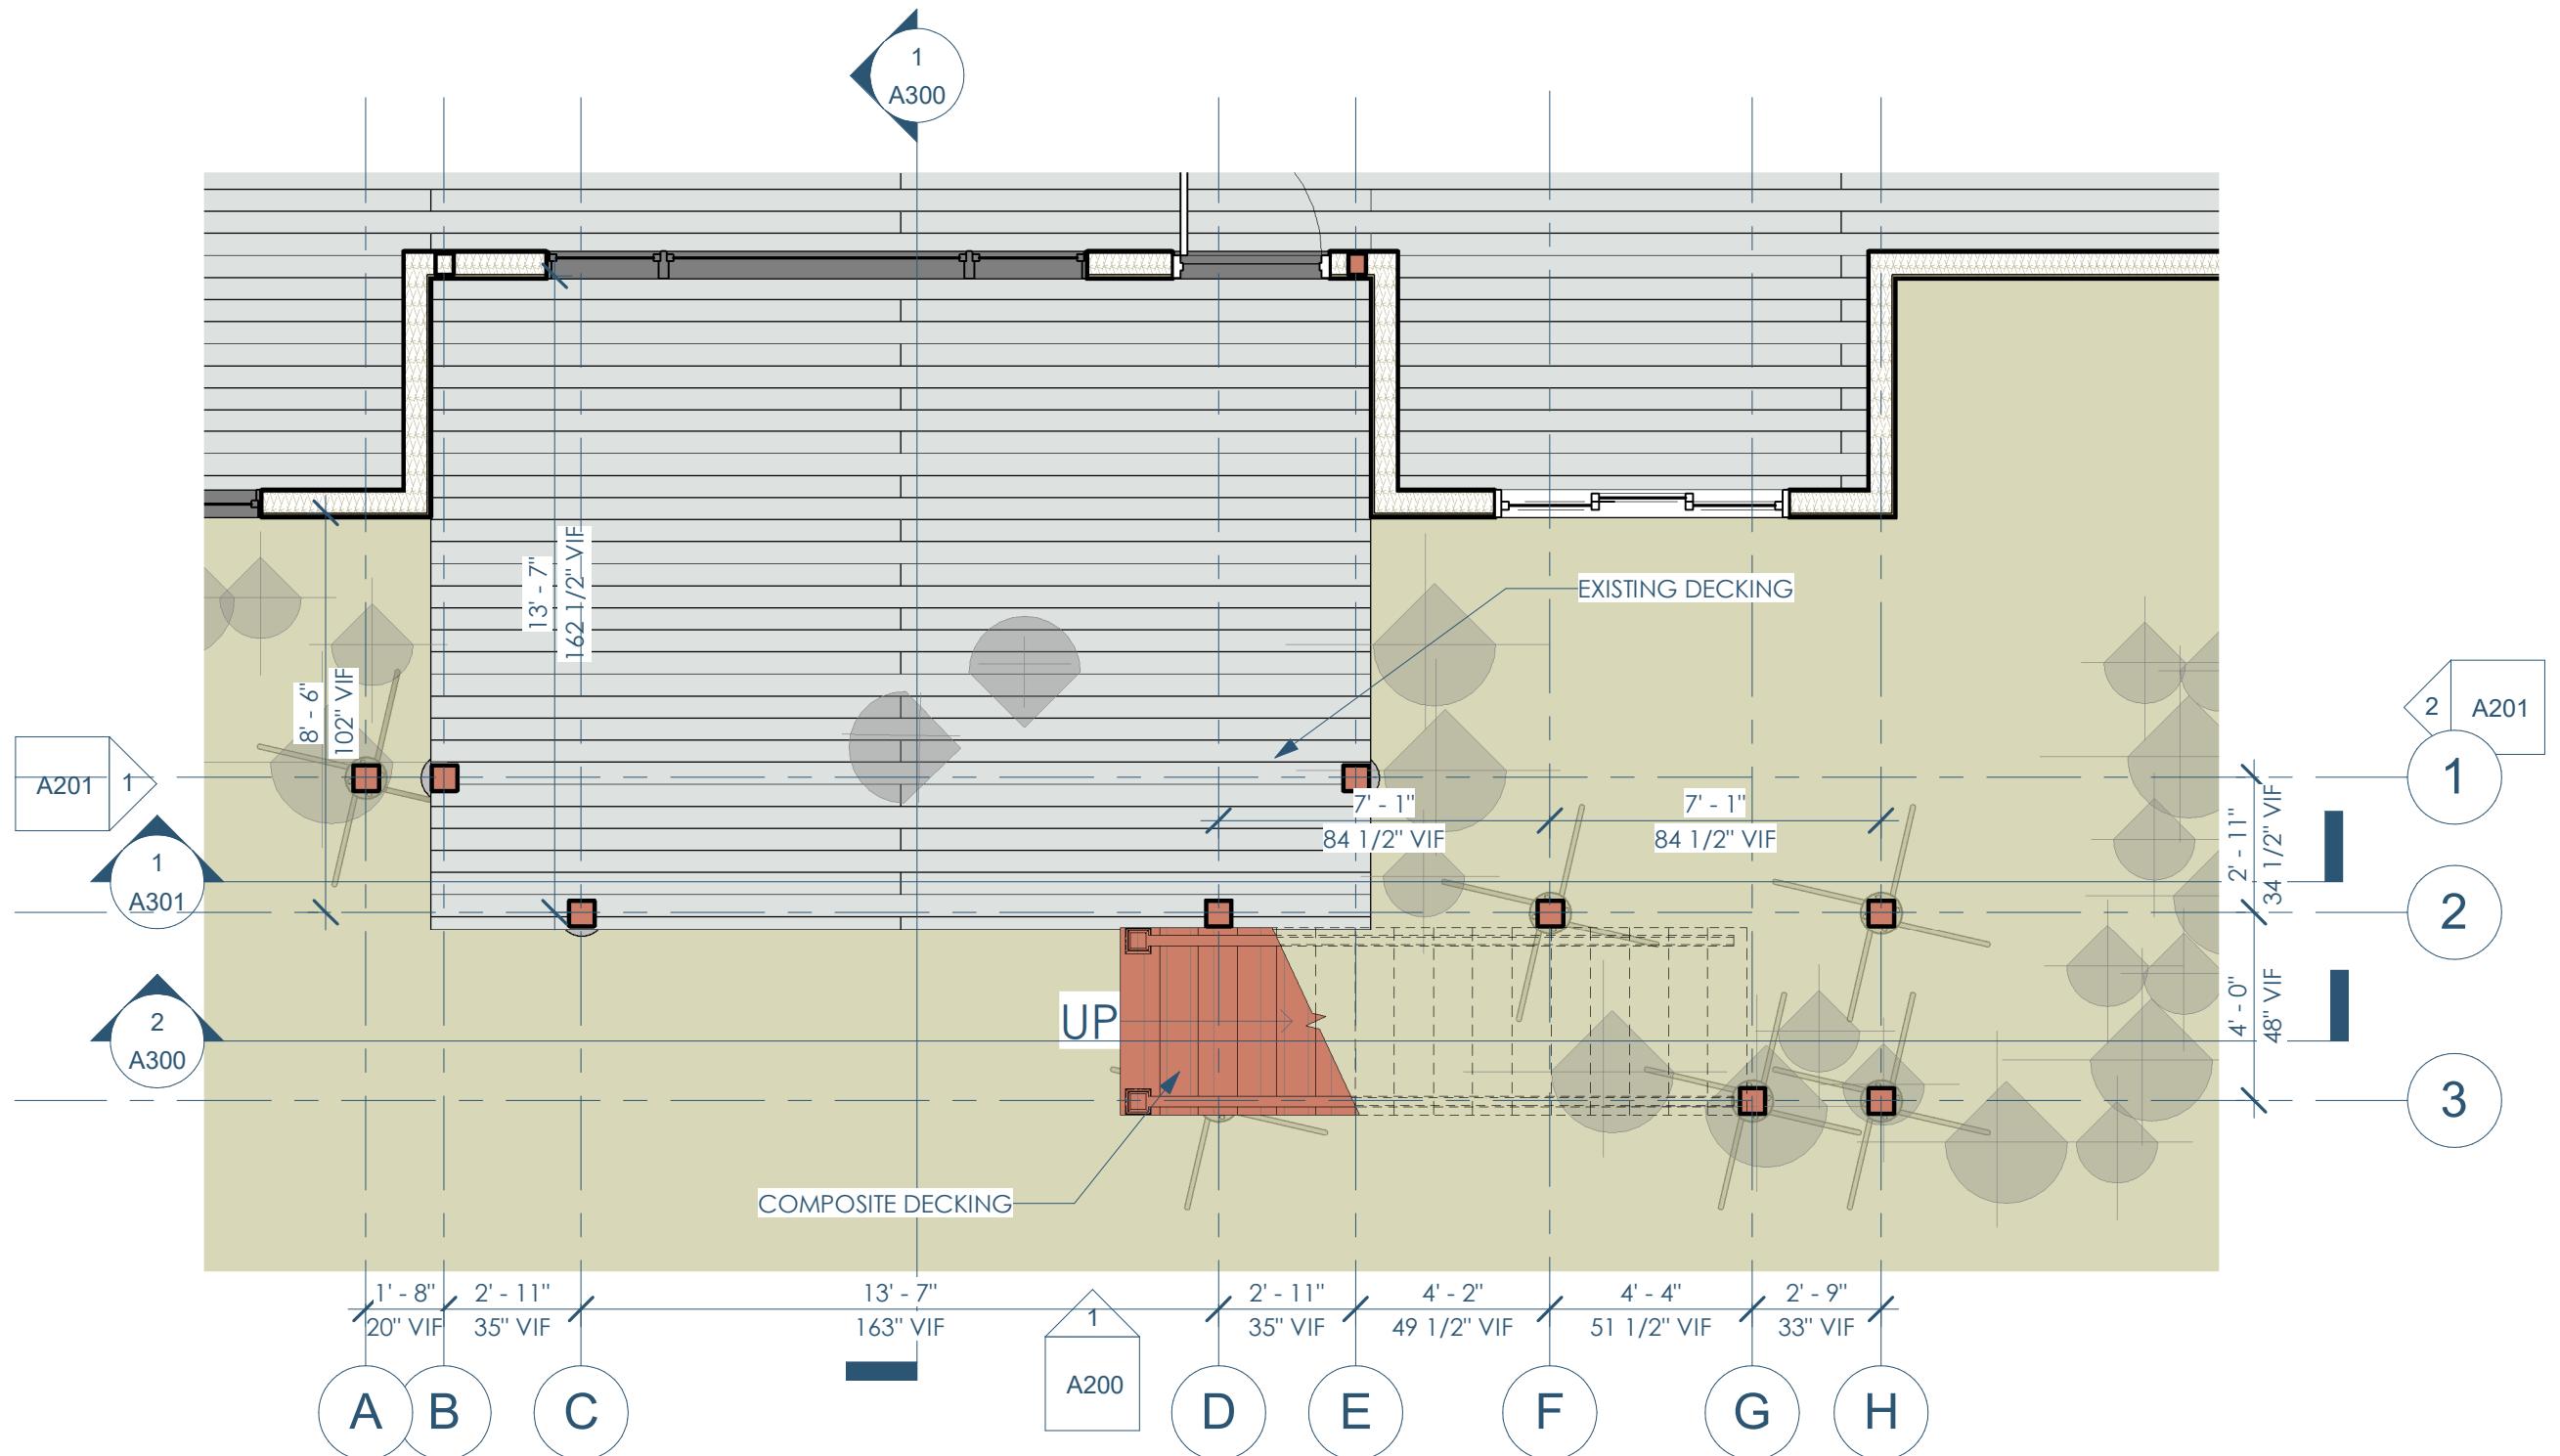

LAKE COUNTRY
CONSTRUCTION GROUP

General Contractor: Lake Country Construction Group
161 Horizon Dr. | Verona, WI 53593
608.845.1398



Architect: OpeningDesign

316 W Washington Ave. | Suite 675 | Madison, WI 53703
ryan@openingdesign.com | 773.425.6456

HERNAN RESIDENCE - 05.29.2018
453 MATTERHORN DR - VERONA WI 53593
FLOOR PLANS - 1ST FLOOR - (A100)



1

2

3

C

C

B

B

A

A

1A FLOOR PLAN - 2ND FLOOR
1/4" = 1'-0"

LAKE COUNTRY
CONSTRUCTION GROUP

General Contractor: Lake Country Construction Group
161 Horizon Dr. | Verona, WI 53593
608.845.1398





Architect: OpeningDesign

316 W Washington Ave. | Suite 675 | Madison, WI 53703
ryan@openingdesign.com | 773.425.6456



HERNAN RESIDENCE - 05.29.2018
453 MATTERHORN DR - VERONA WI 53593
FLOOR PLAN - 2ND FLOOR - (A102)

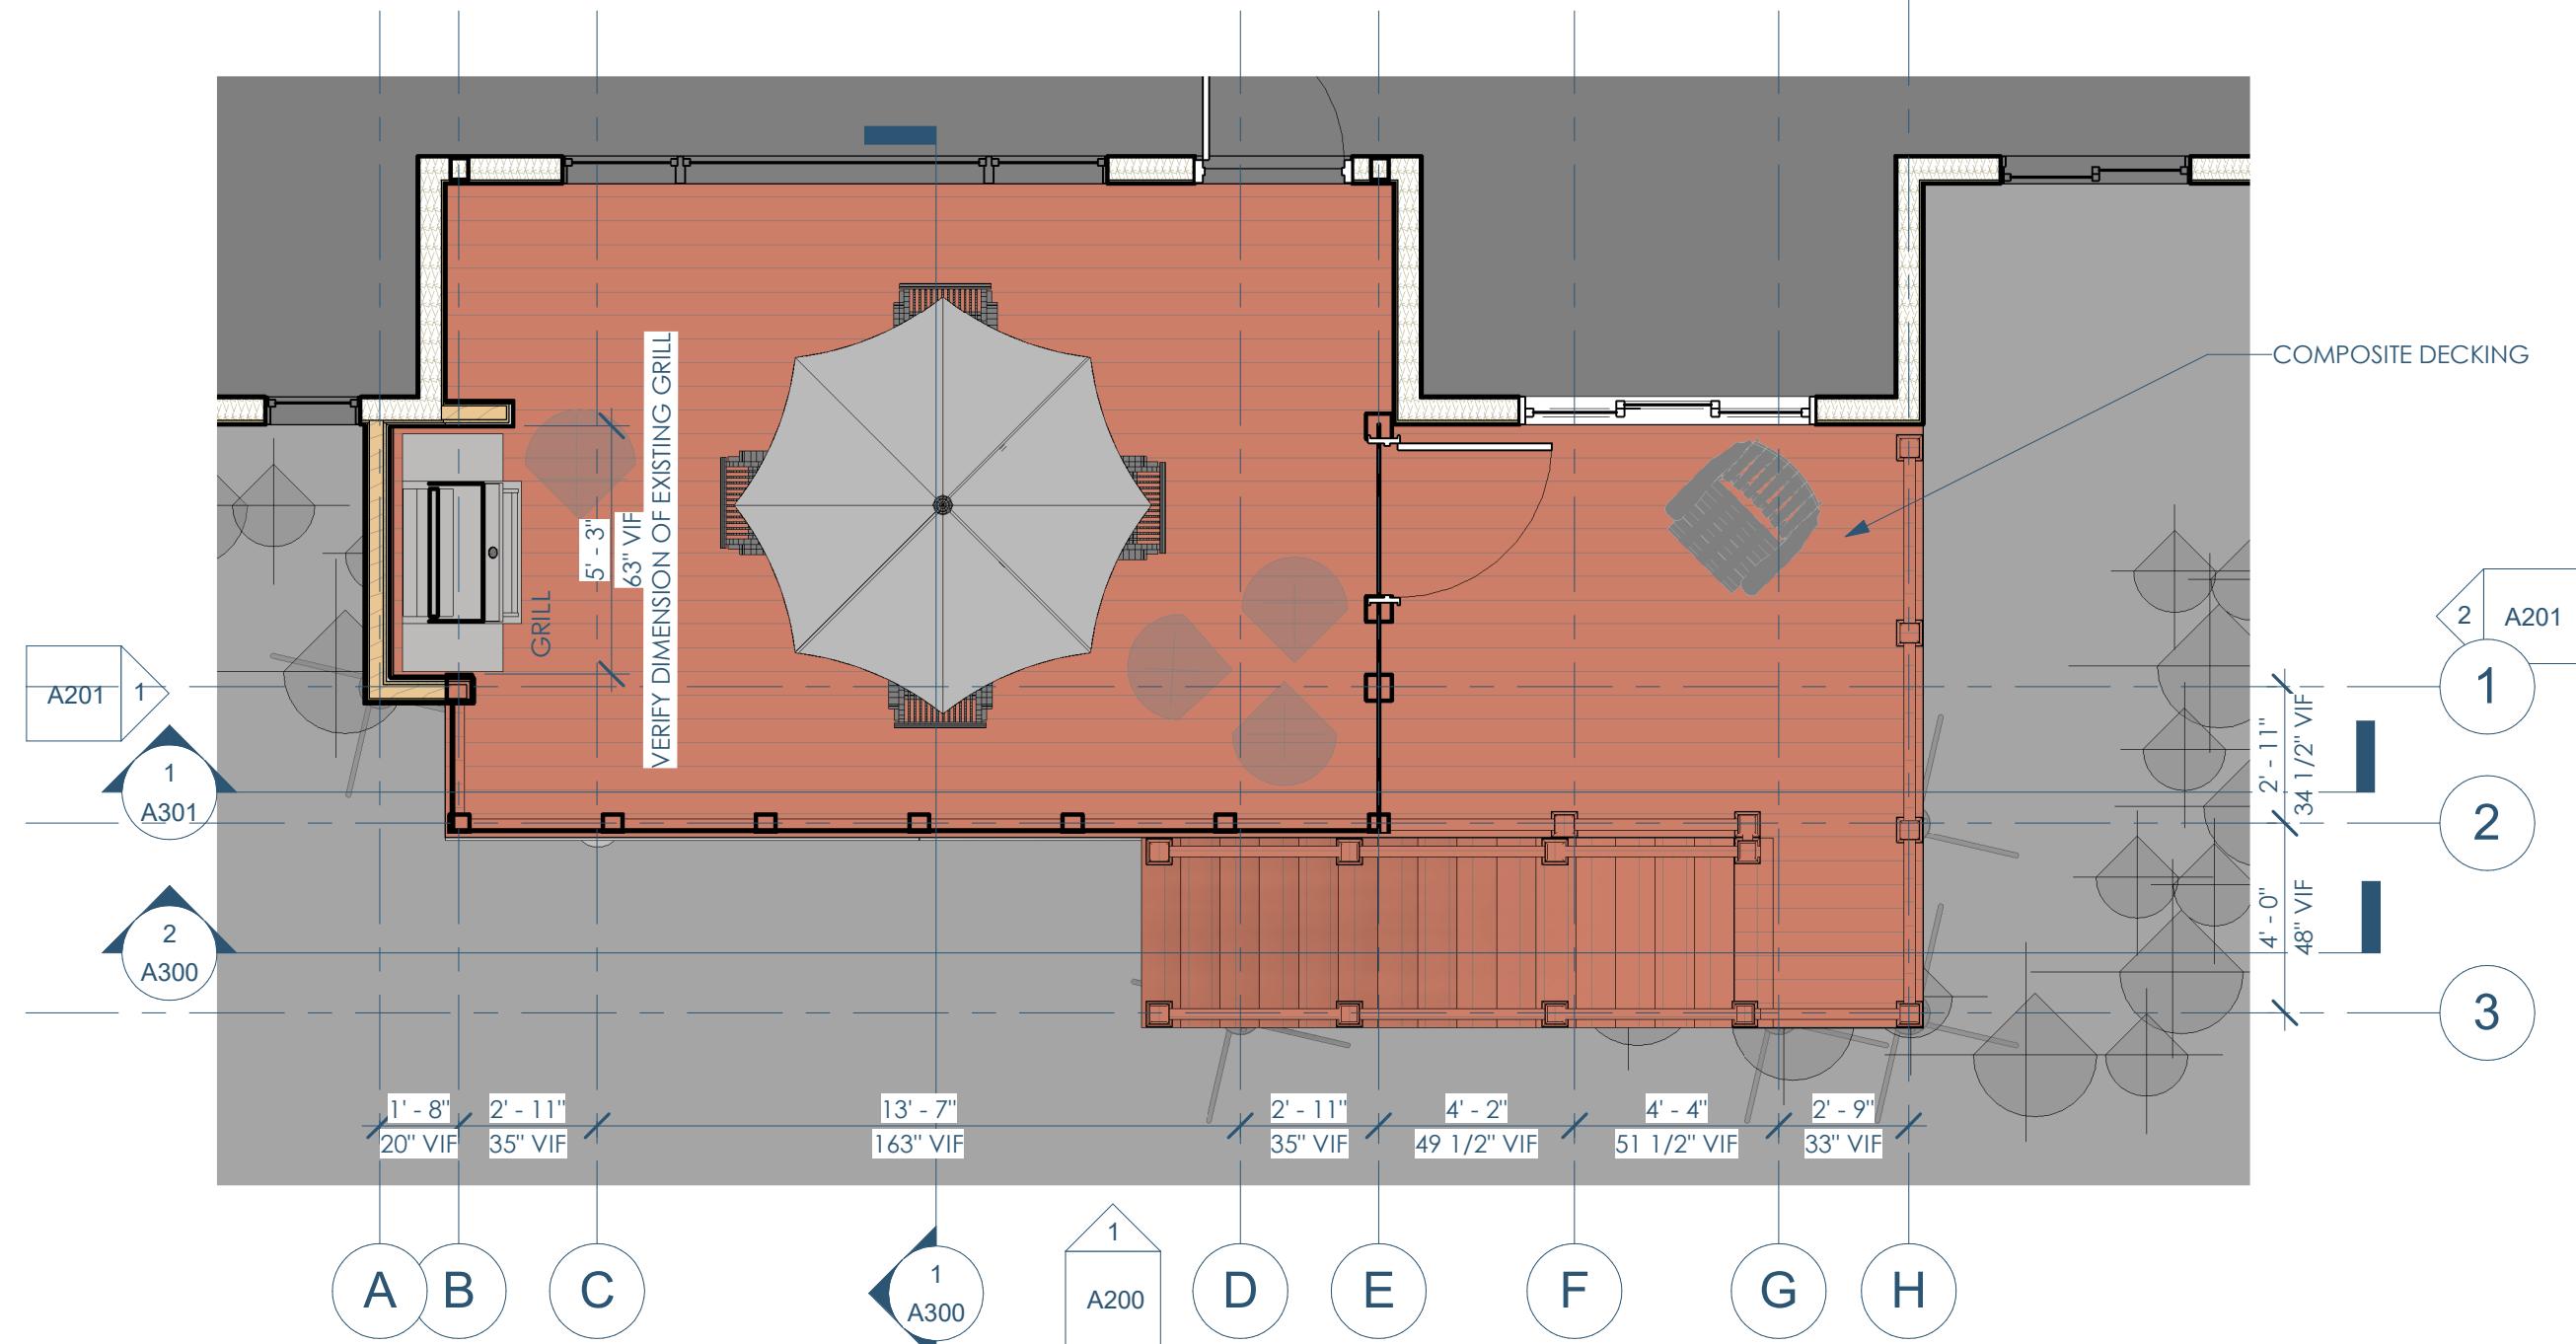

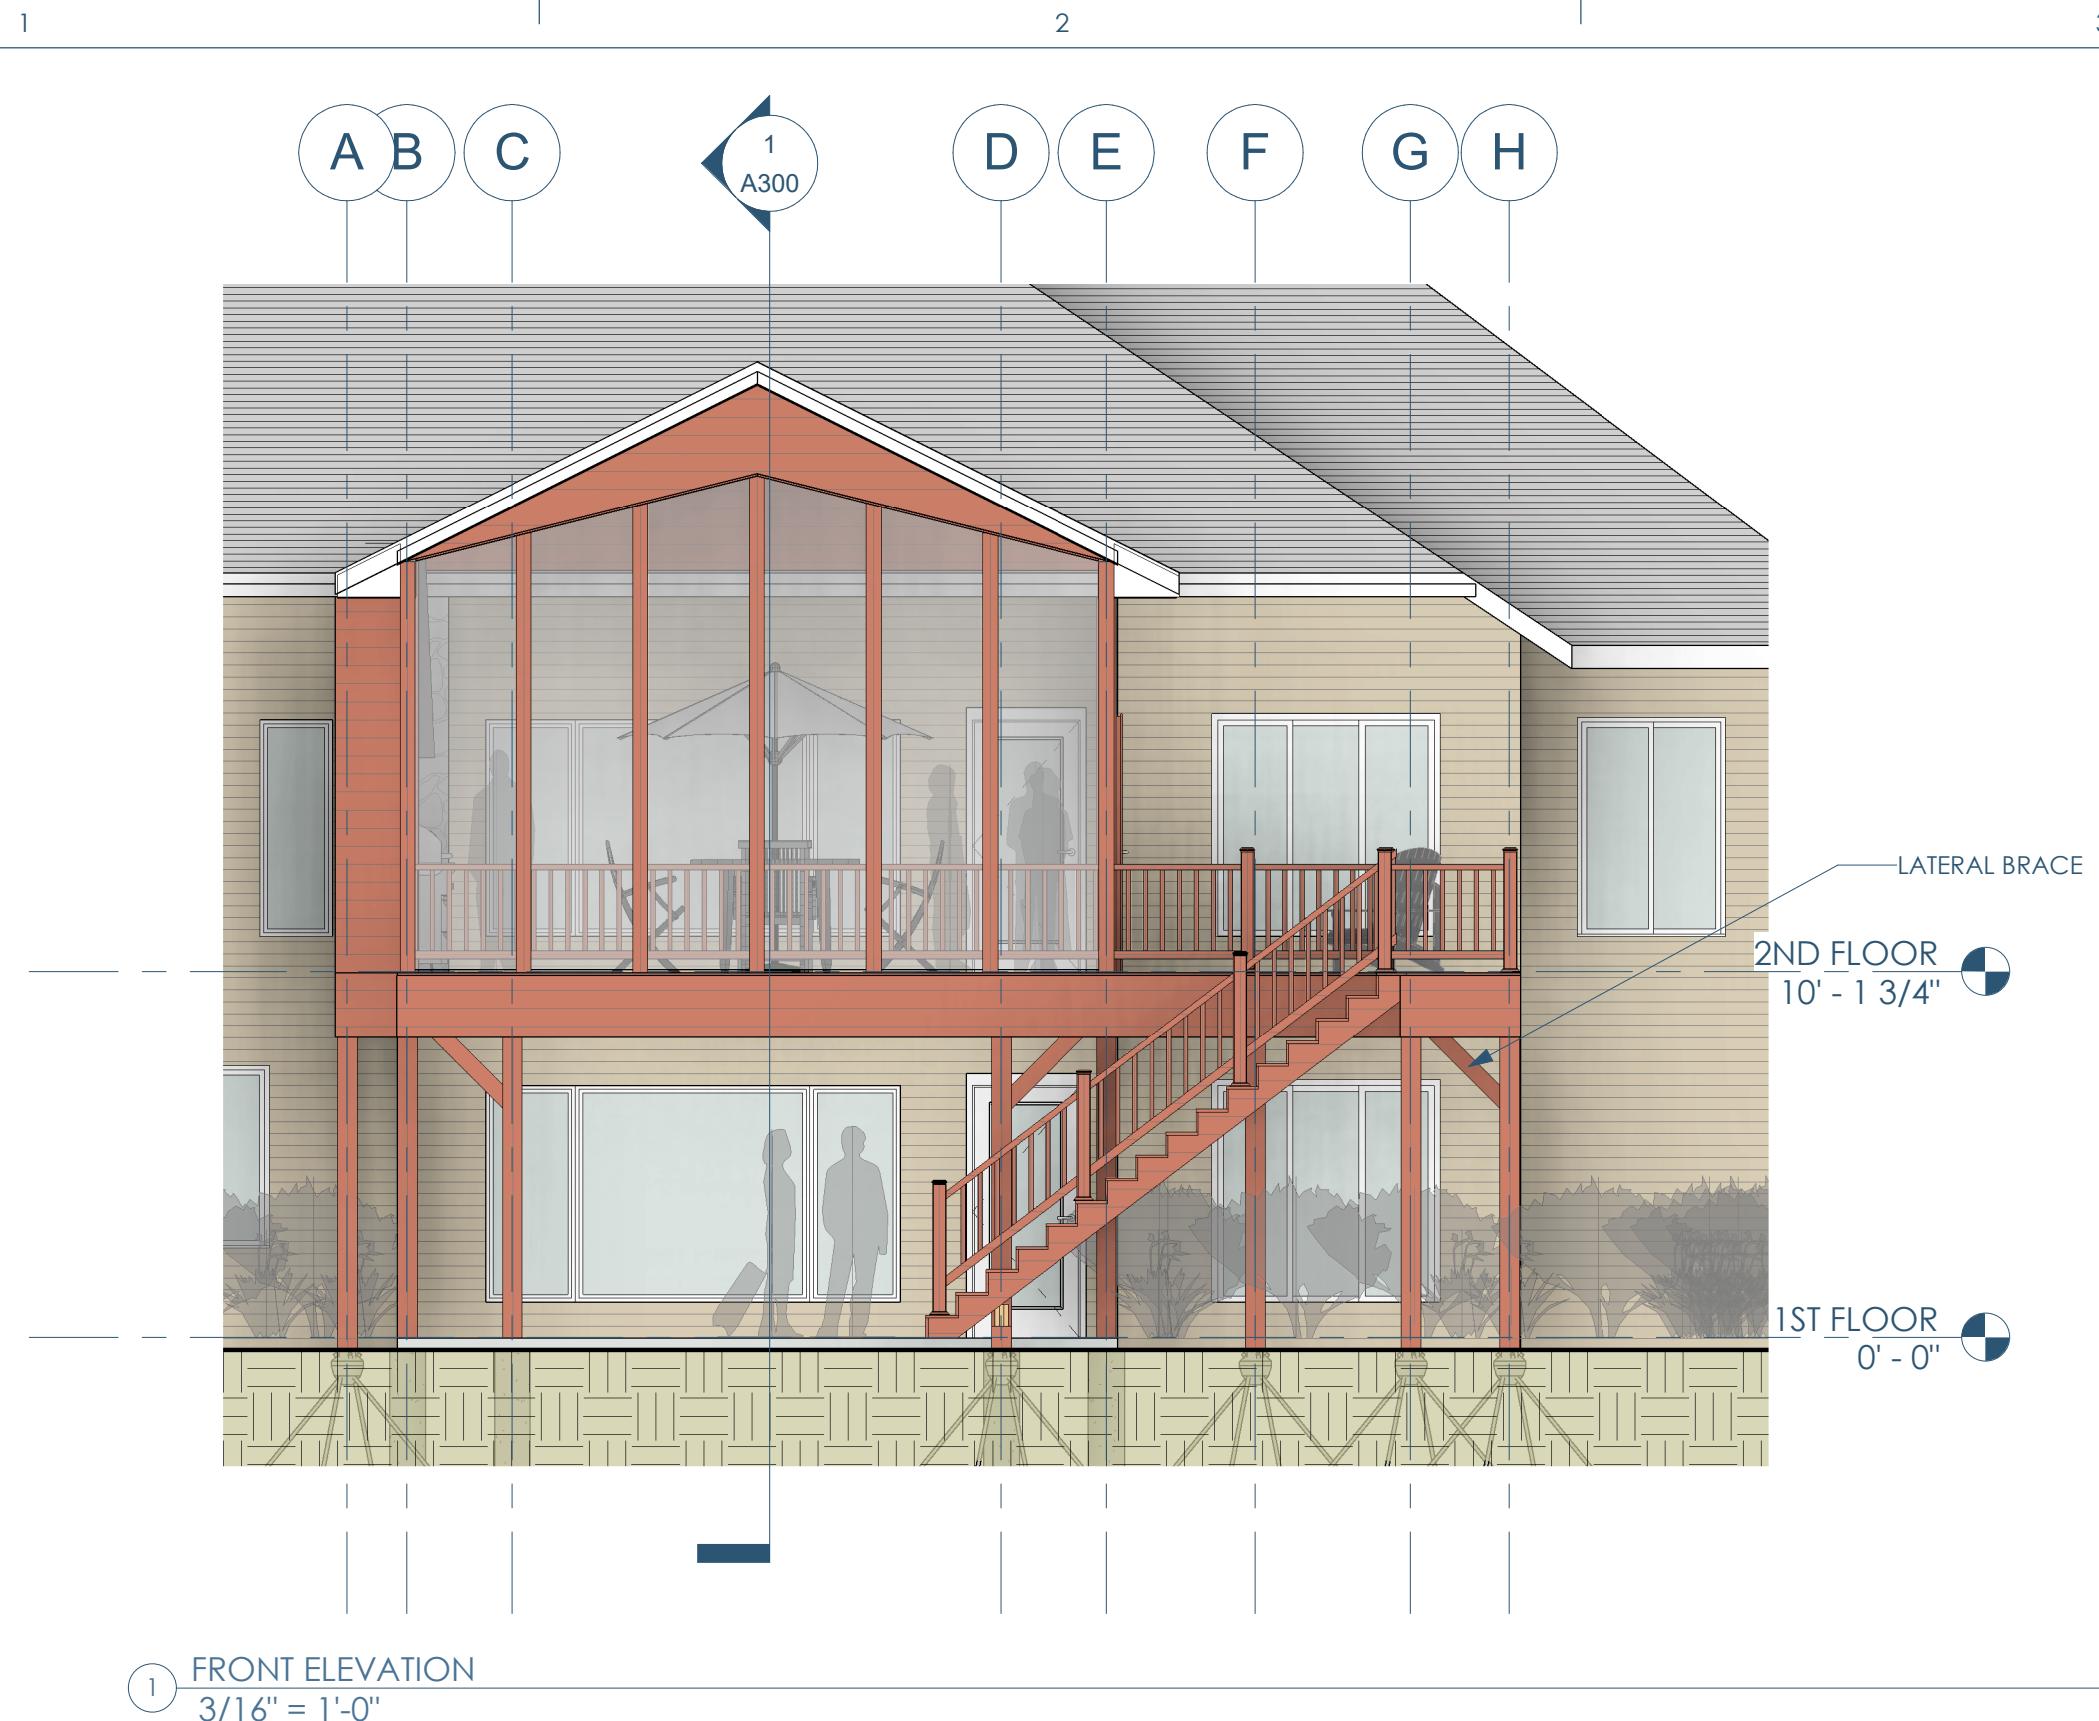

**LAKE COUNTRY
CONSTRUCTION GROUP**

General Contractor: Lake Country Construction Group
161 Horizon Dr. | Verona, WI 53593
608.845.1398





Architect: OpeningDesign

316 W Washington Ave. | Suite 675 | Madison, WI 53703
ryan@openingdesign.com | 773.425.6456

0 4' 8' 12'

HERNAN RESIDENCE - 05.29.2018
453 MATTERHORN DR - VERONA WI 53593
BUILDING ELEVATIONS - (A200)

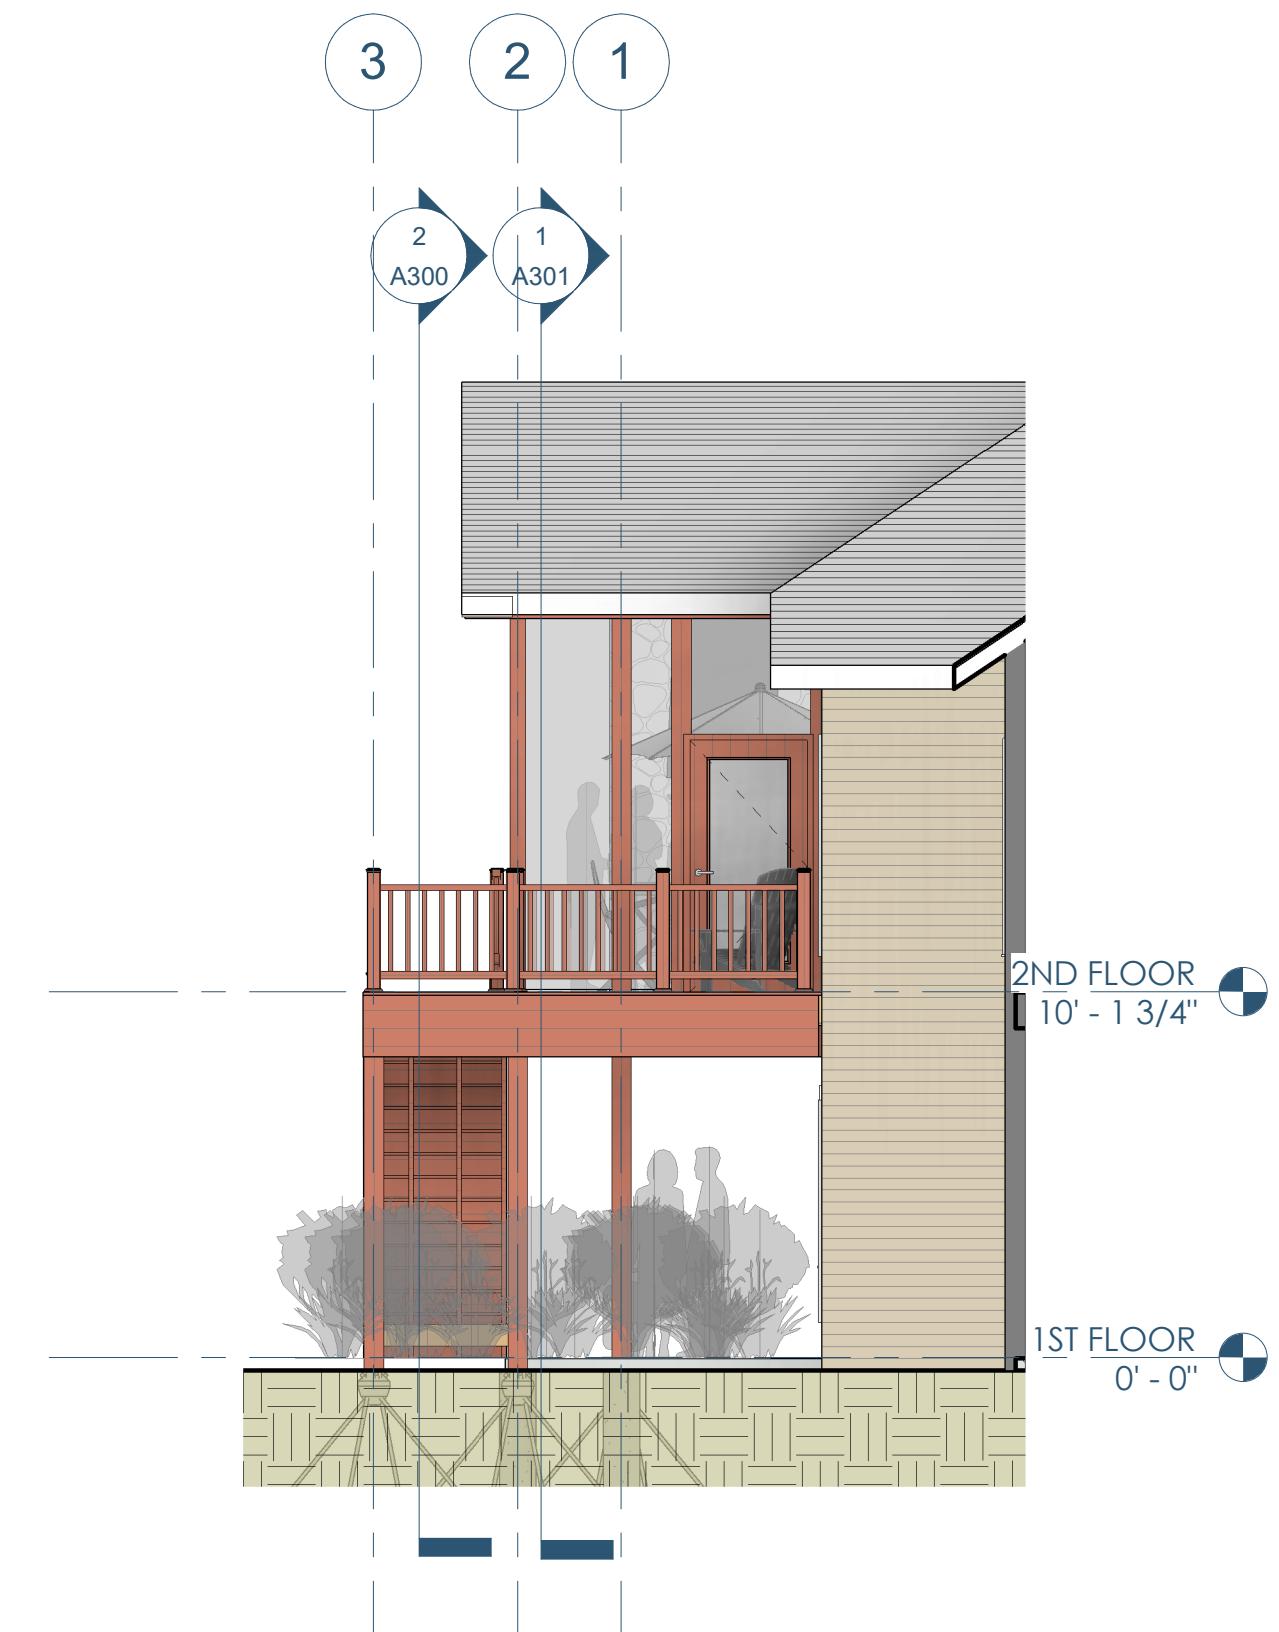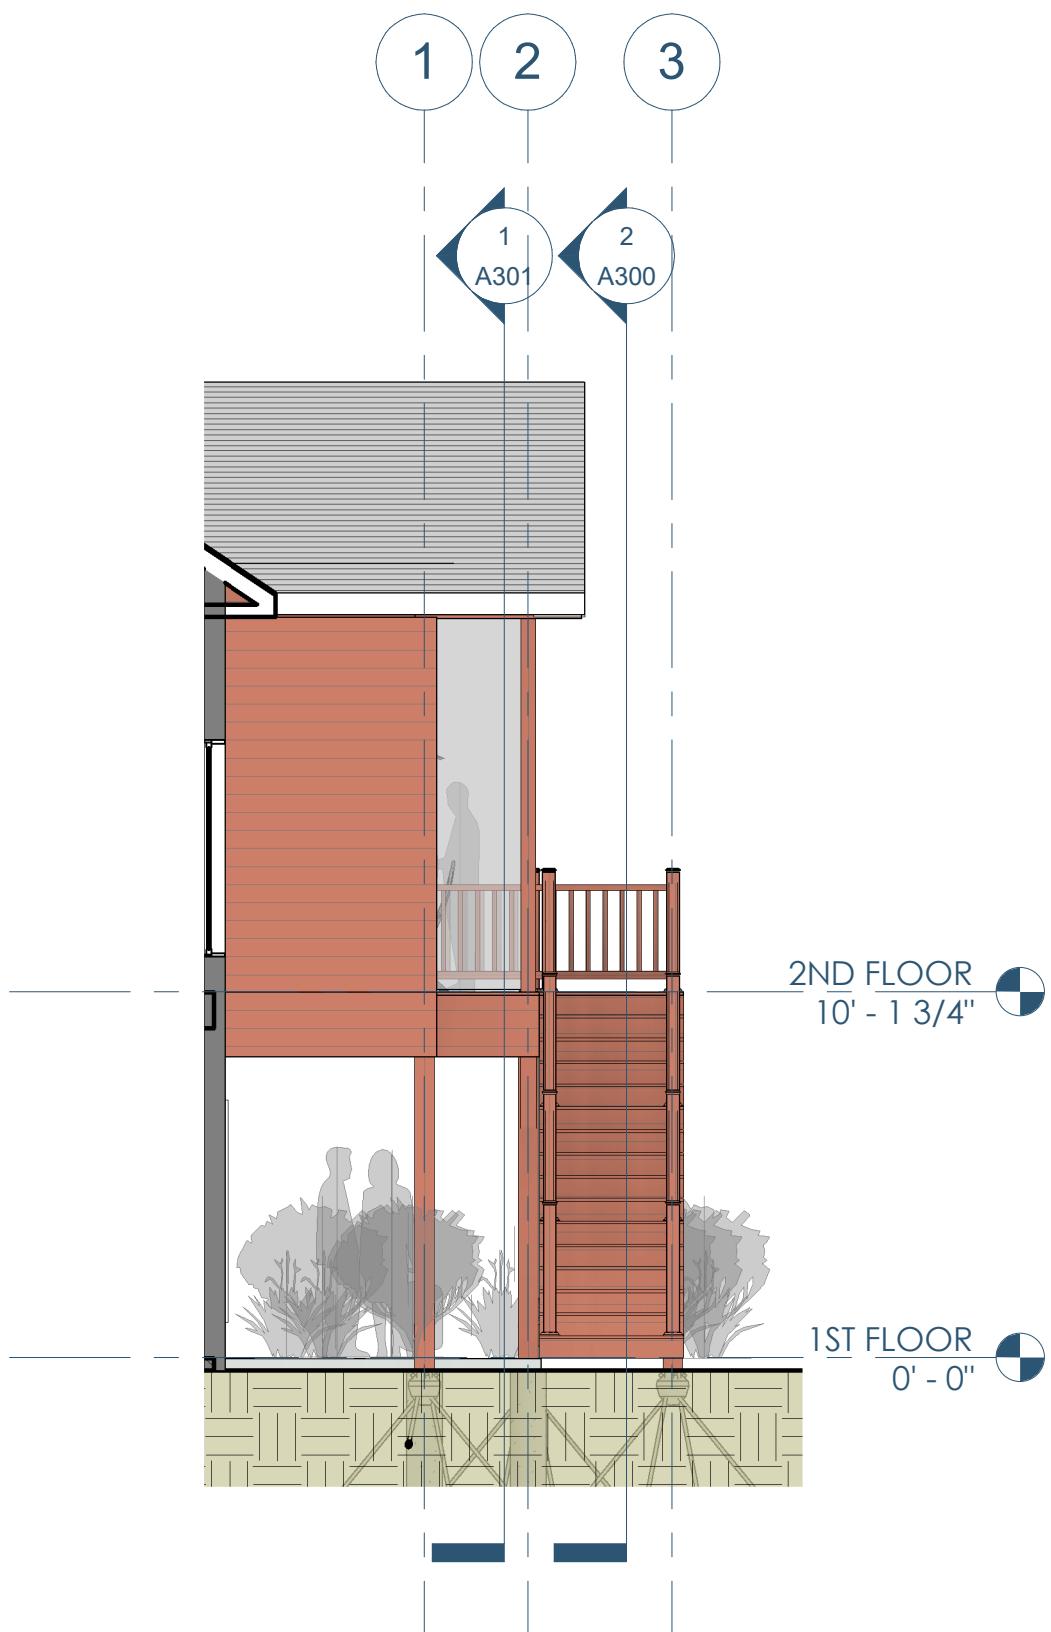

0 4' 8' 12'


General Contractor: Lake Country Construction Group
161 Horizon Dr. | Verona, WI 53593
608.845.1398

Architect: OpeningDesign
316 W Washington Ave. | Suite 675 | Madison, WI 53703
ryan@openingdesign.com | 773.425.6456

LAKE COUNTRY
CONSTRUCTION GROUP




HERNAN RESIDENCE - 05.29.2018
453 MATTERHORN DR - VERONA, WI 53593
BUILDING ELEVATIONS - (A201)

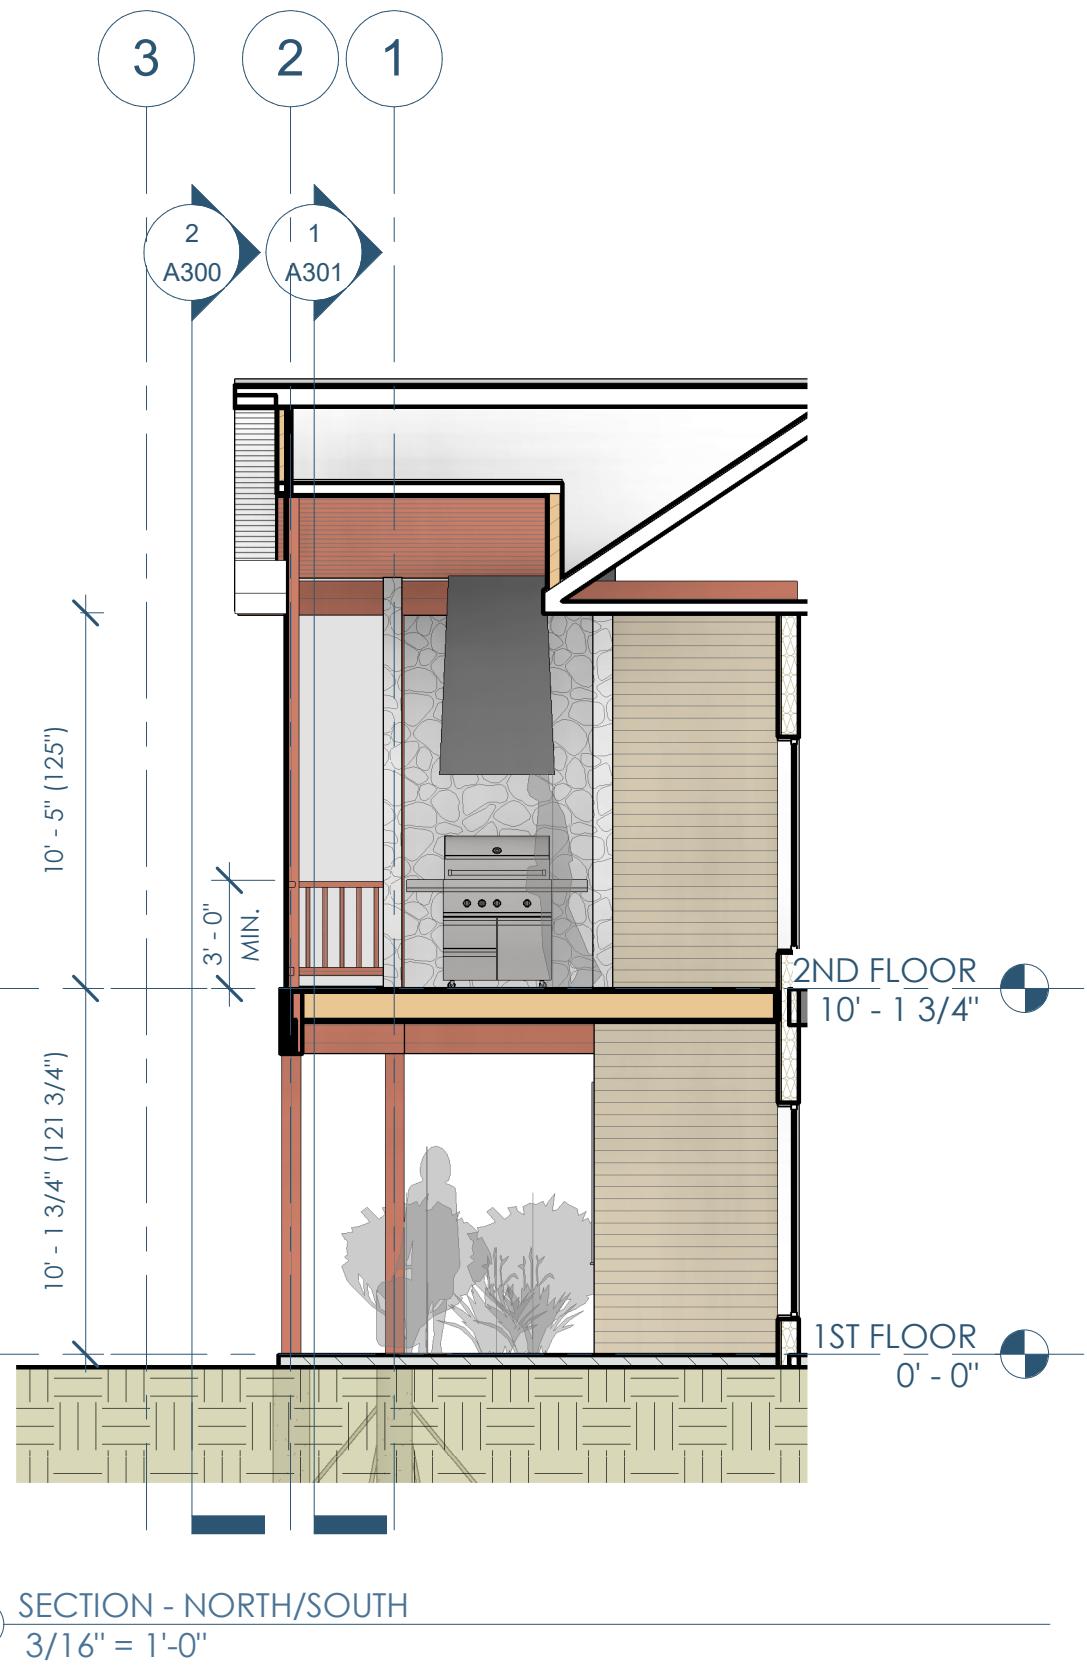

General Contractor: Lake Country Construction Group
161 Horizon Dr. | Verona, WI 53593
608.845.1398

Architect: OpeningDesign
316 W Washington Ave. | Suite 675 | Madison, WI 53703
ryan@openingdesign.com | 773.425.6456

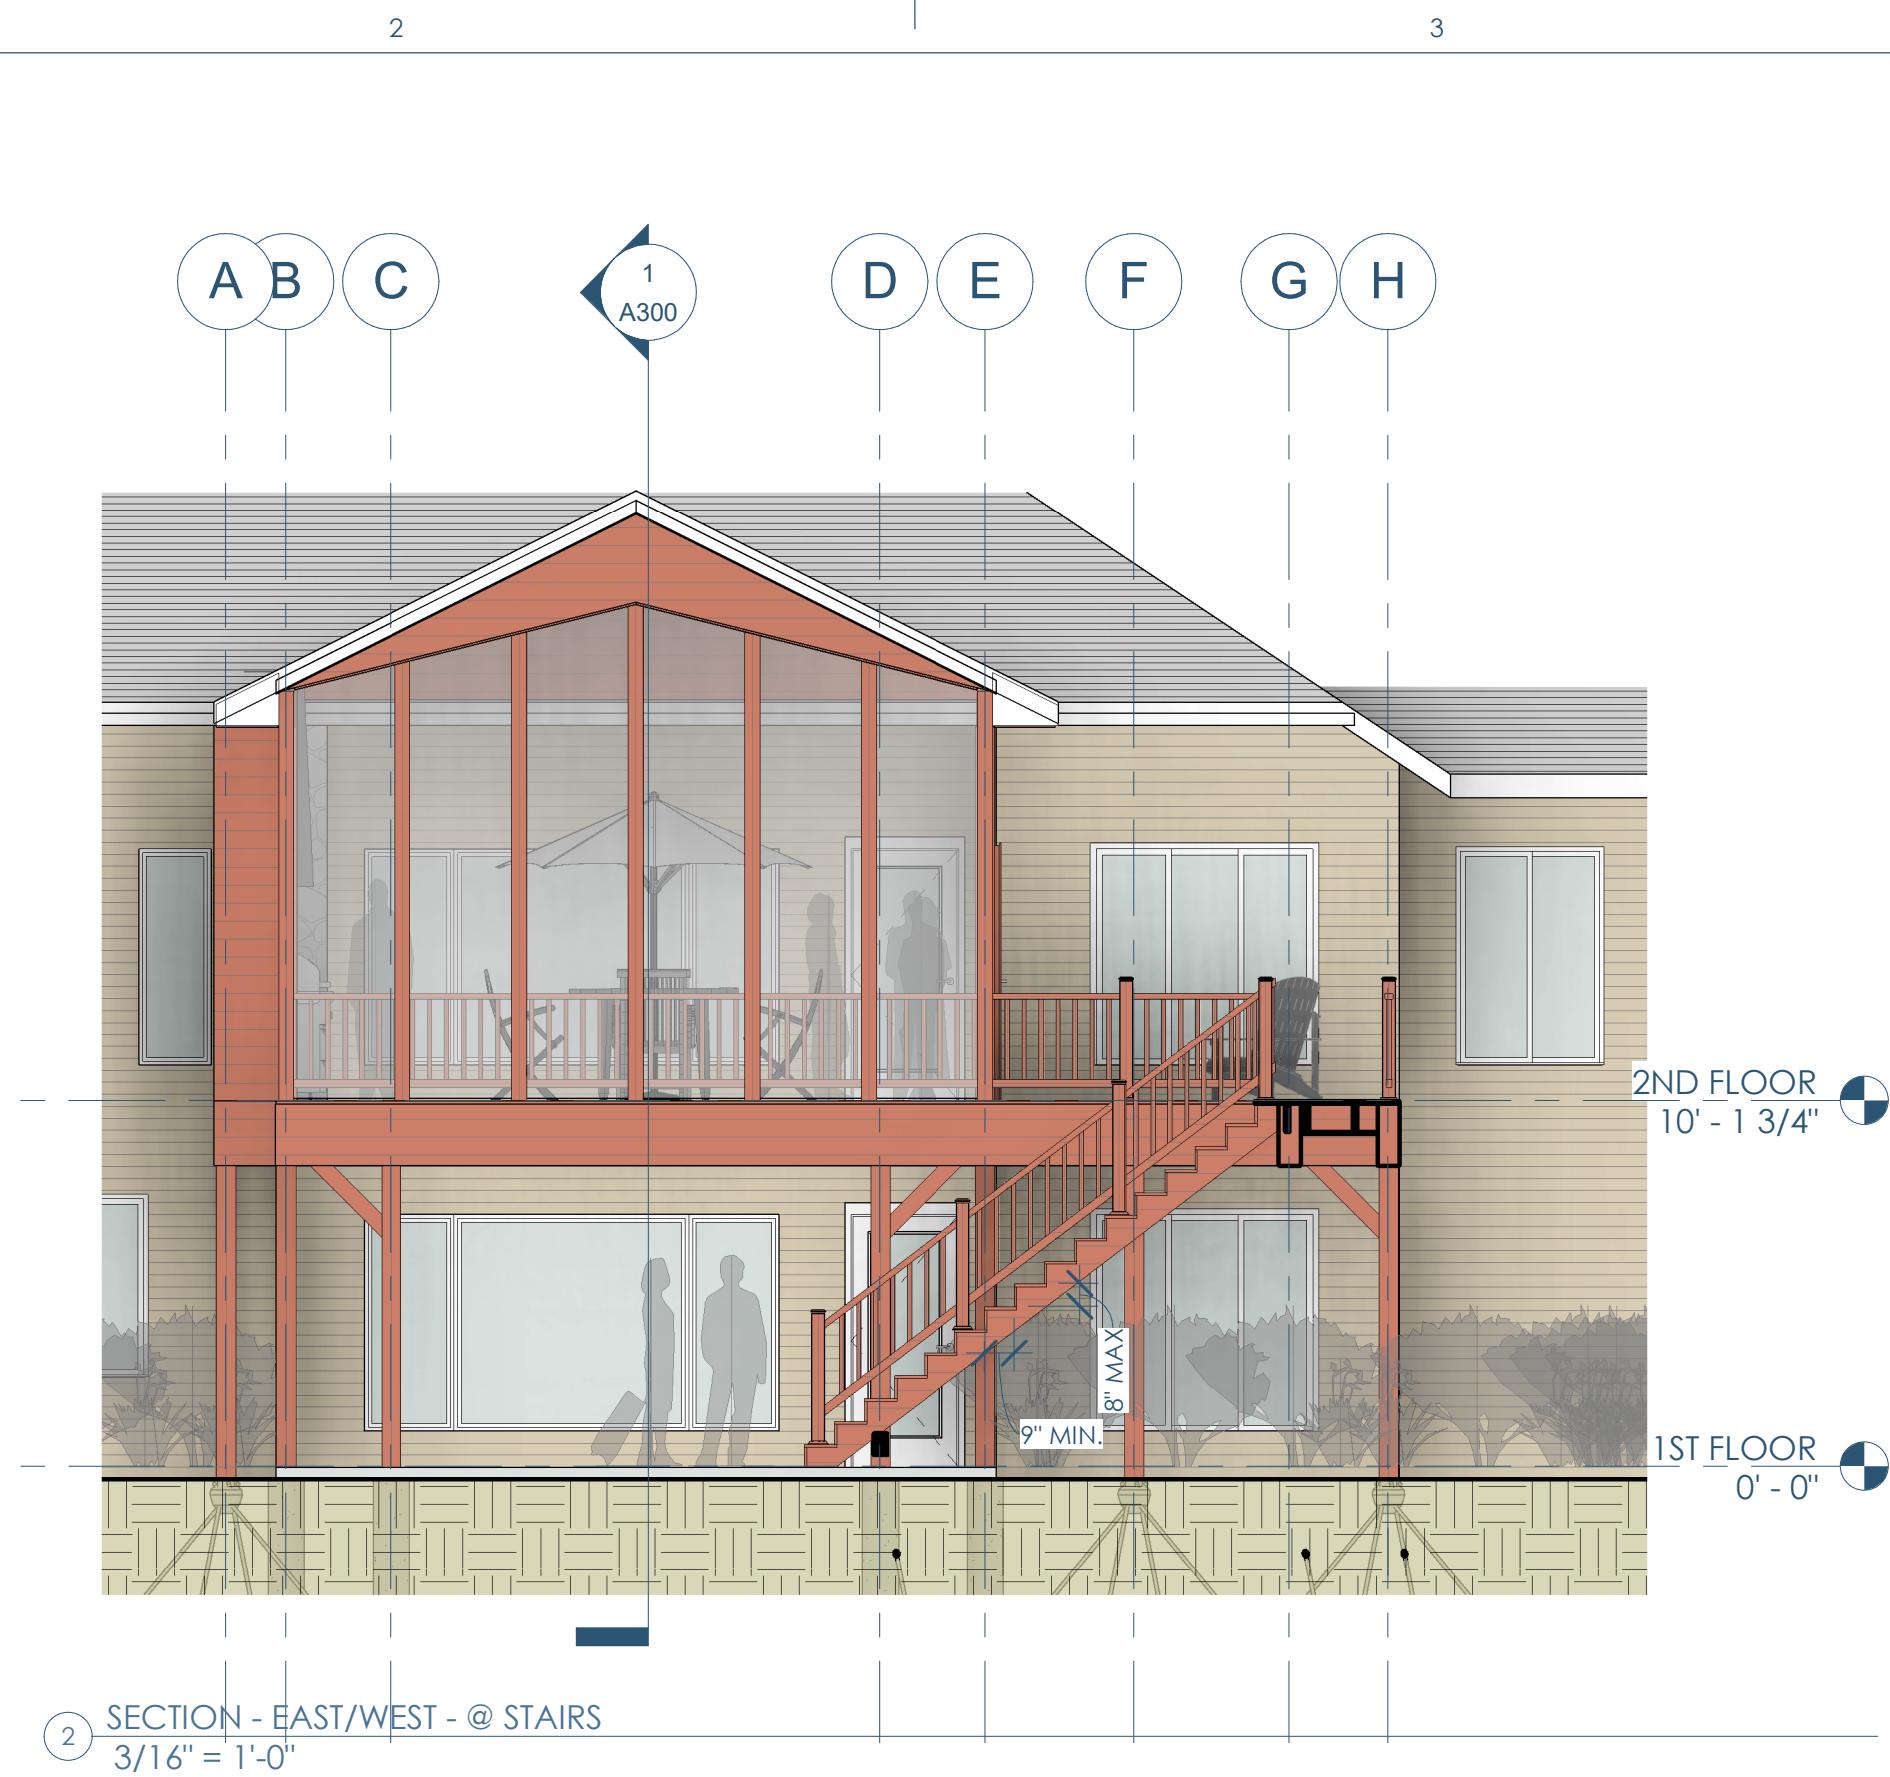

HERNAN RESIDENCE - 05.29.2018
453 MATTERHORN DR - VERONA, WI 53593
BUILDING SECTIONS - (A300)

1

2

3

① SECTION - EAST/WEST
3/16" = 1'-0"

LAKE COUNTRY
CONSTRUCTION GROUP


General Contractor: Lake Country Construction Group
161 Horizon Dr. | Verona, WI 53593
608.845.1398



Architect: OpeningDesign

316 W Washington Ave. | Suite 675 | Madison, WI 53703
ryan@openingdesign.com | 773.425.6456

HERNAN RESIDENCE - 05.29.2018
453 MATTERHORN DR - VERONA WI 53593
BUILDING SECTION - (A301)

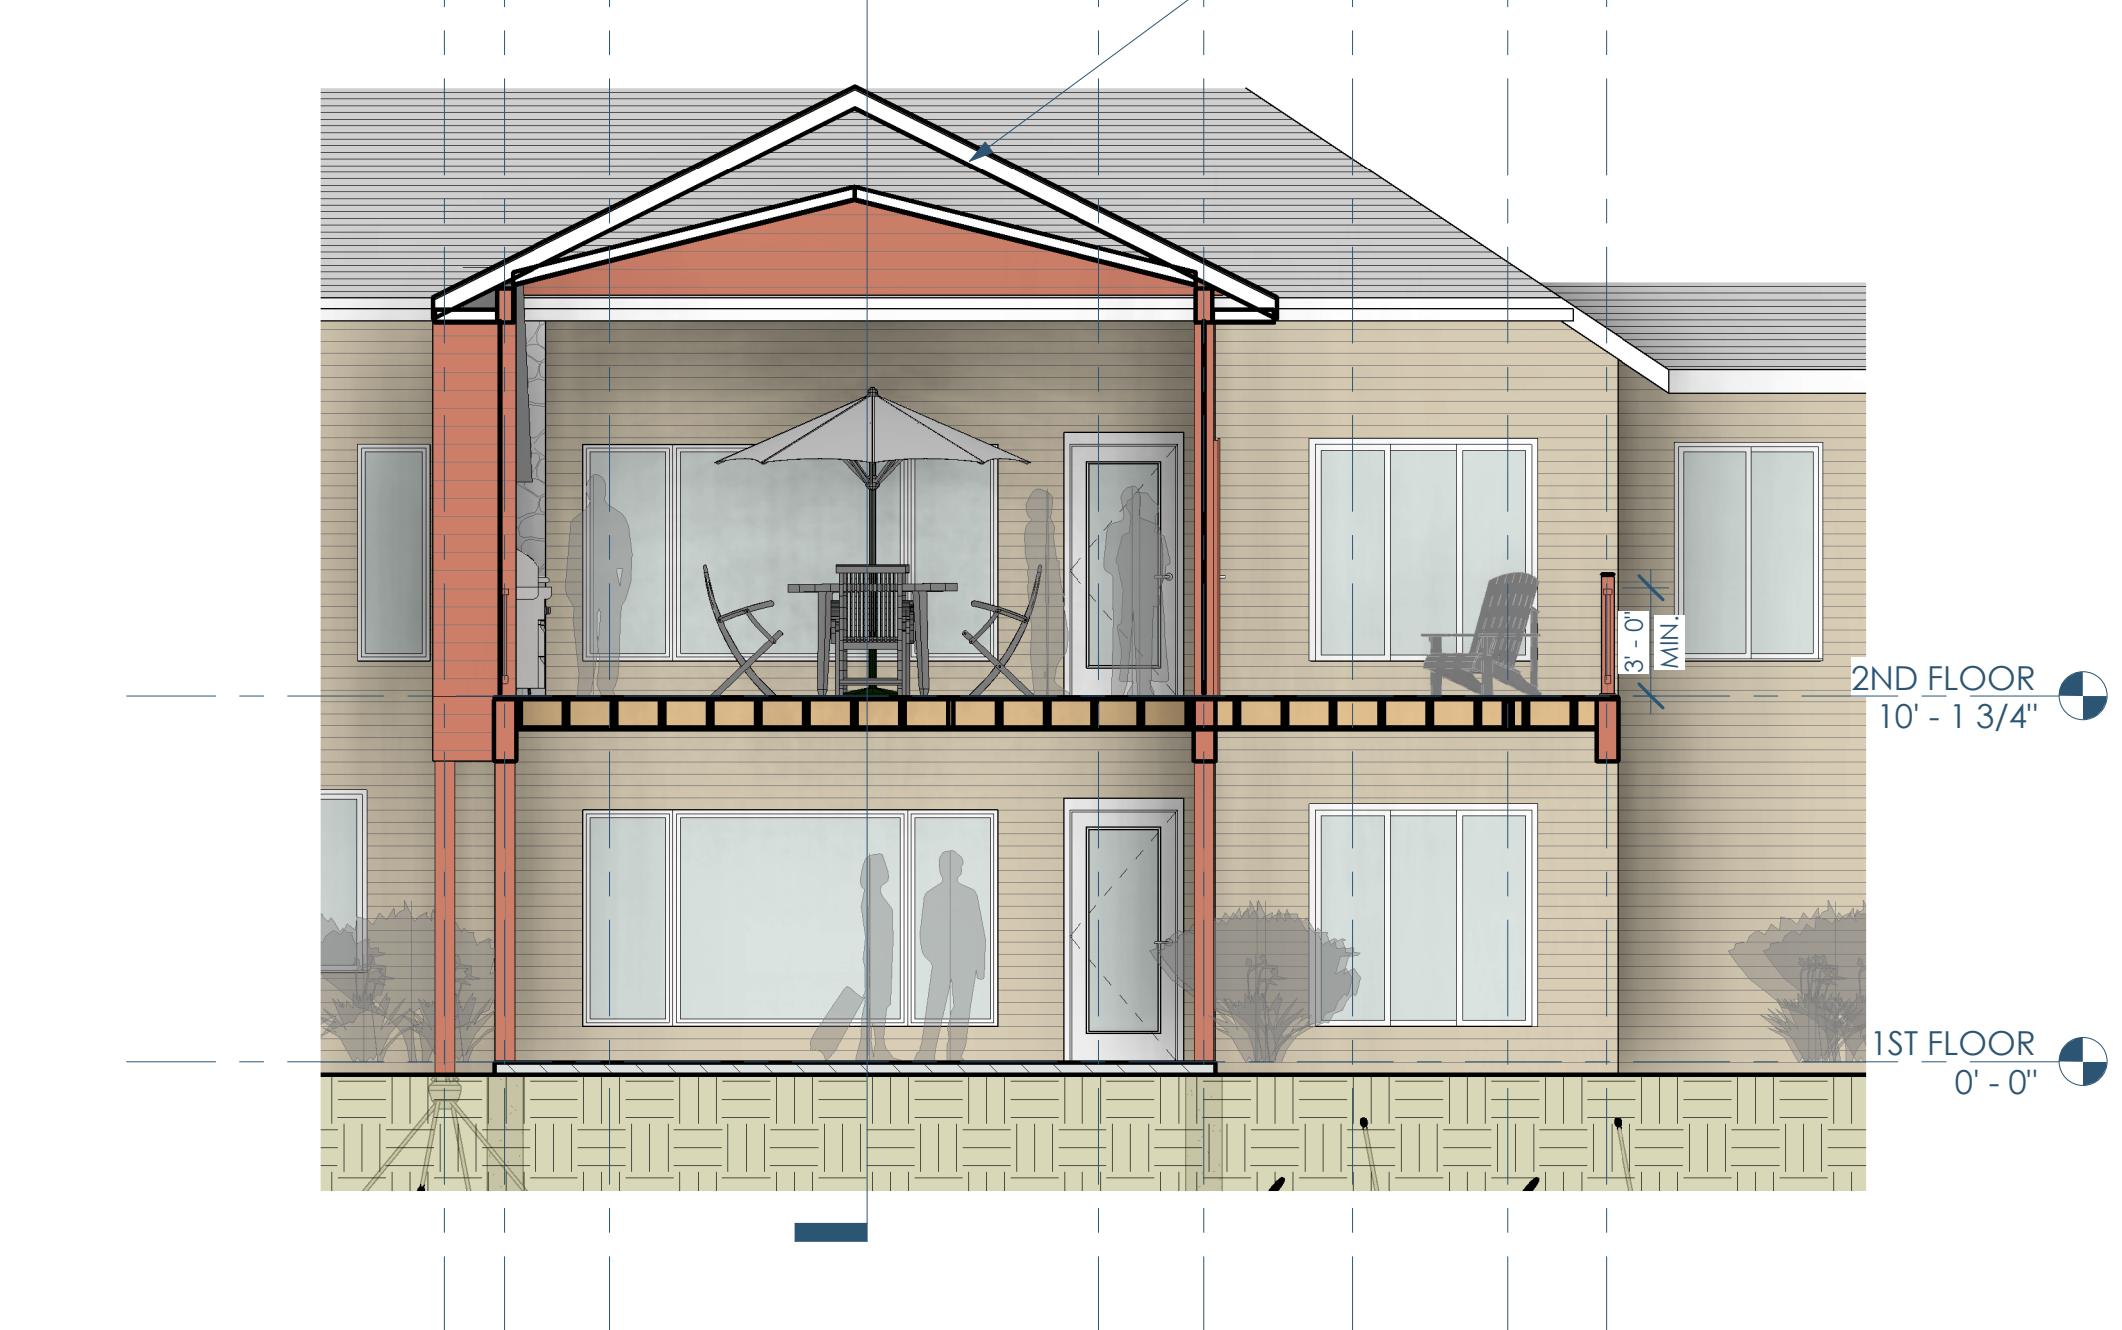



① PERSPECTIVE 1



② PERSPECTIVE 2


**LAKE COUNTRY
CONSTRUCTION GROUP**

General Contractor: Lake Country Construction Group
161 Horizon Dr. | Verona, WI 53593
608.845.1398



Architect: OpeningDesign
316 W Washington Ave. | Suite 675 | Madison, WI 53703
ryan@openingdesign.com | 773.425.6456

HERNAN RESIDENCE - 05.29.2018
453 MATTERHORN DR - VERONA, WI 53593
3D VIEWS - (A900)

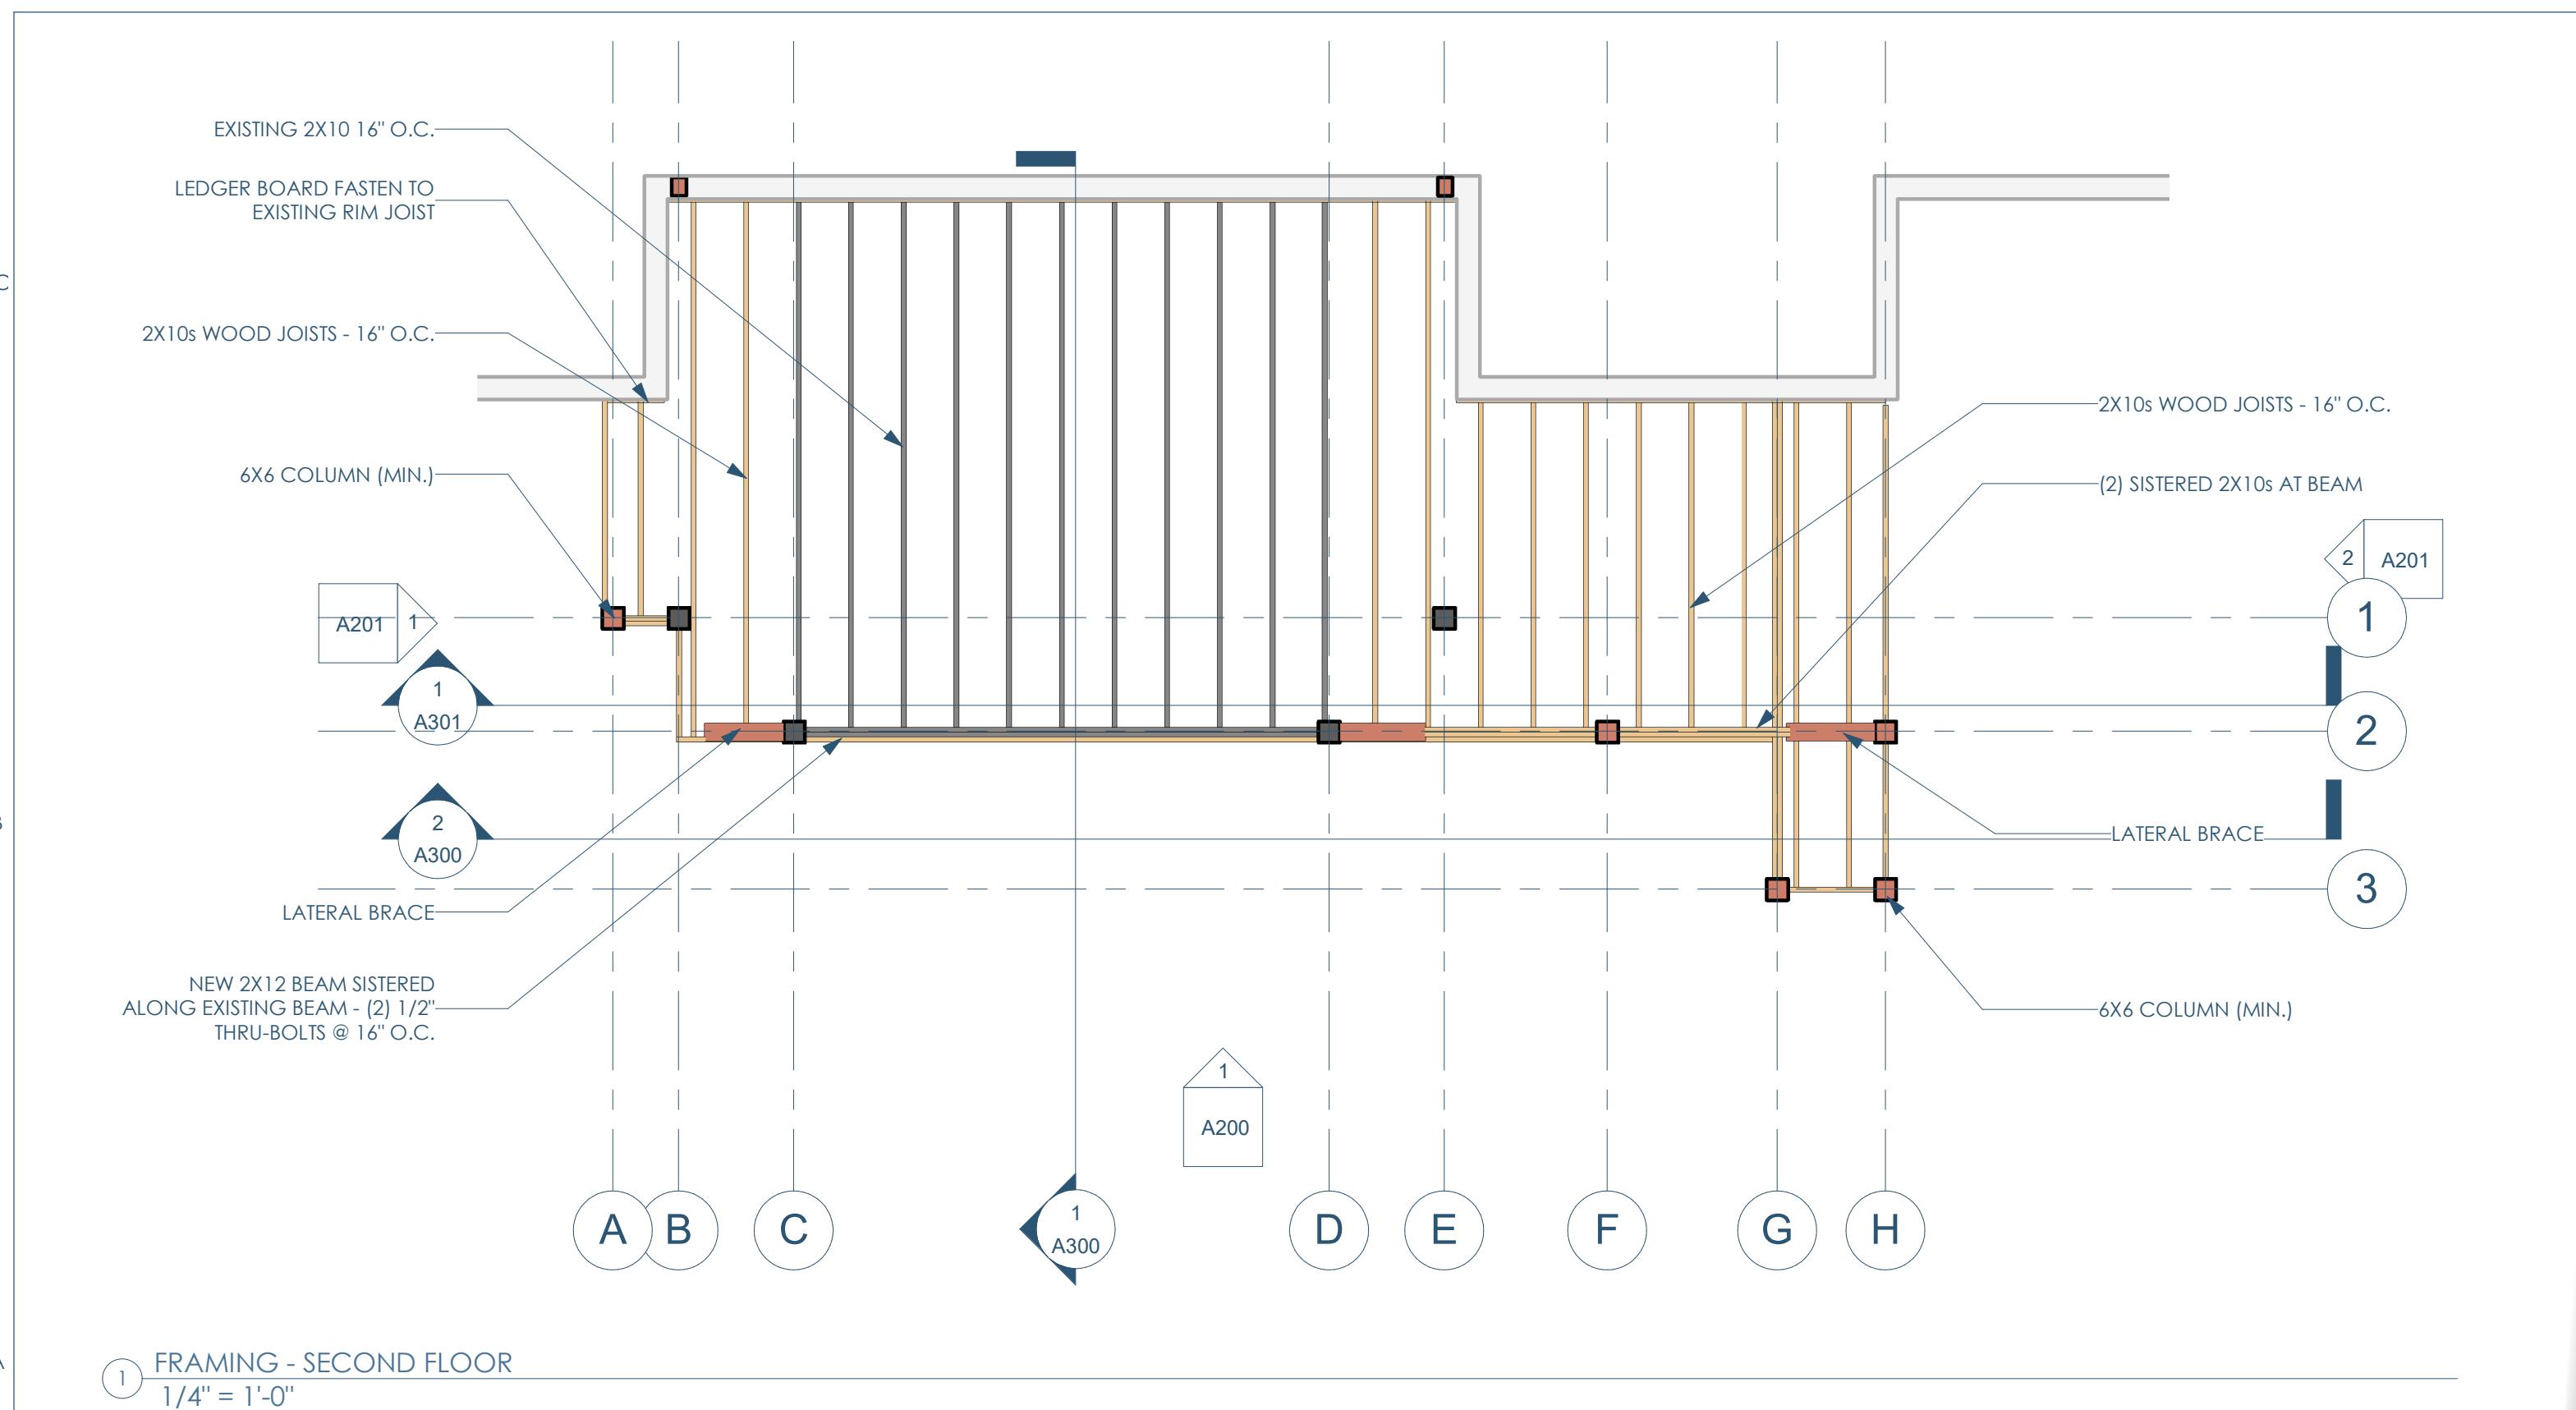

LAKE COUNTRY
CONSTRUCTION GROUP


General Contractor: Lake Country Construction Group
161 Horizon Dr. | Verona, WI 53593
608.845.1398



Architect: OpeningDesign

316 W Washington Ave. | Suite 675 | Madison, WI 53703
ryan@openingdesign.com | 773.425.6456

HERNAN RESIDENCE - 05.29.2018
453 MATTERHORN DR - VERONA WI 53593
FRAMING - (S102)

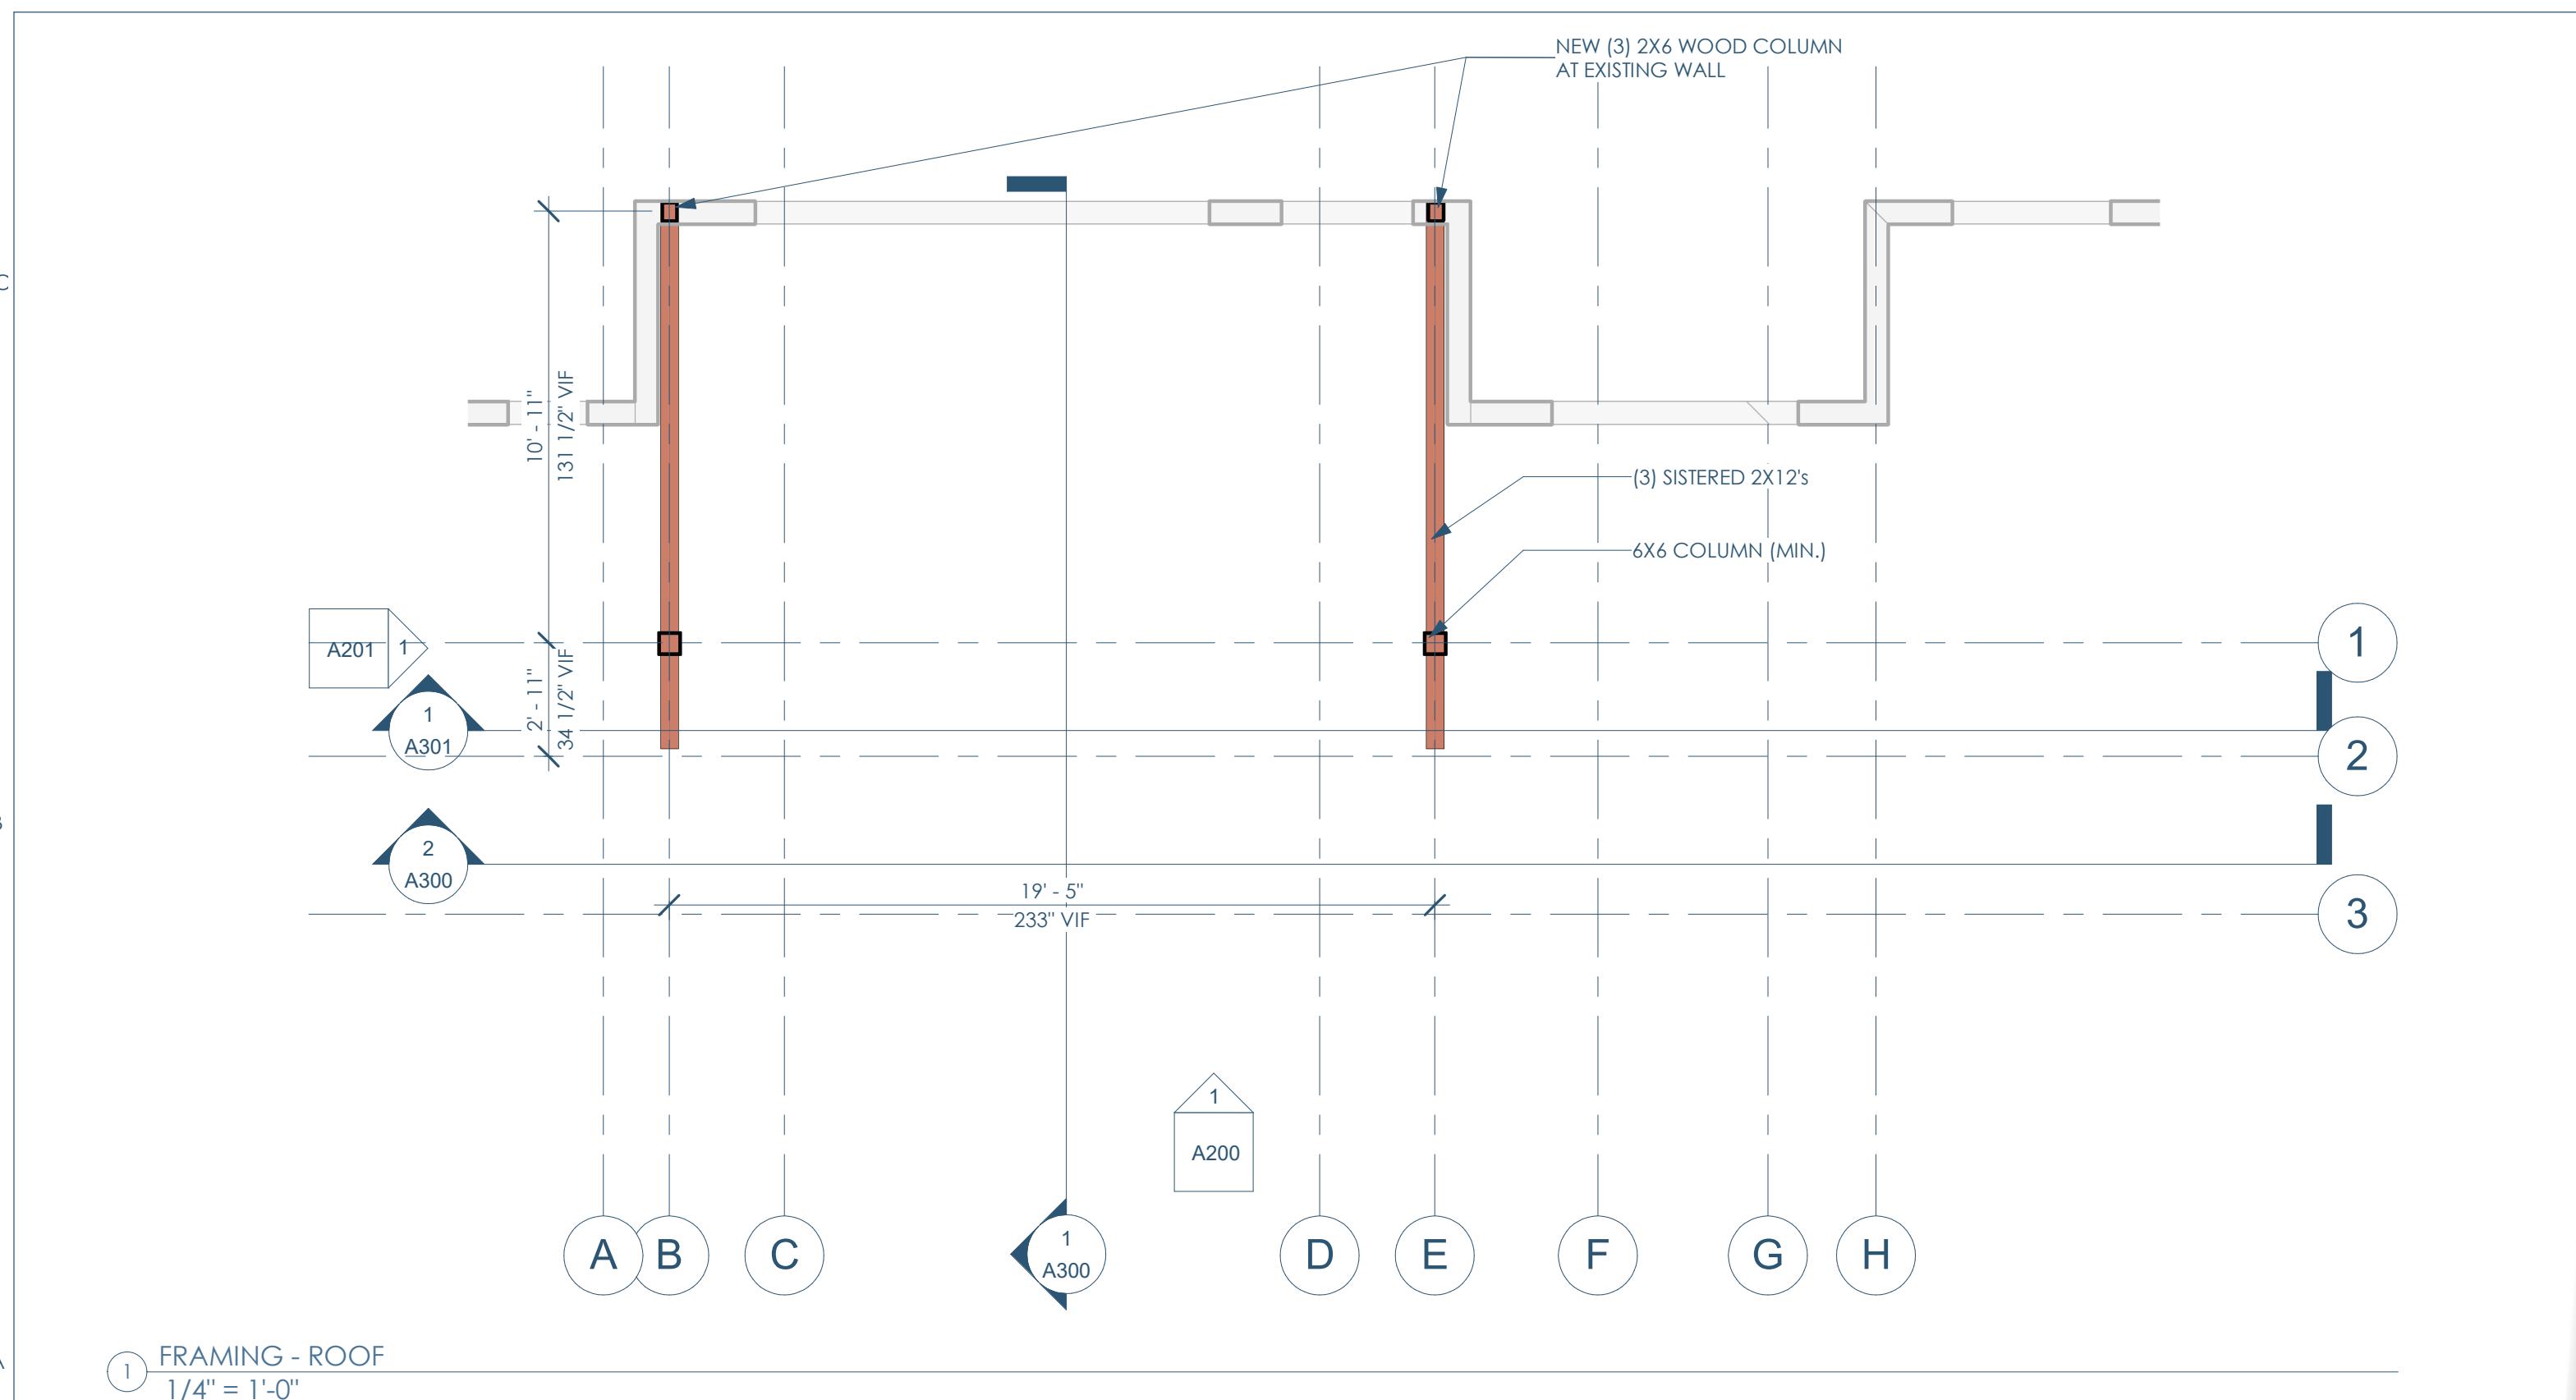

LAKE COUNTRY
CONSTRUCTION GROUP

General Contractor: Lake Country Construction Group
161 Horizon Dr. | Verona, WI 53593
608.845.1398



Architect: OpeningDesign



316 W Washington Ave. | Suite 675 | Madison, WI 53703
ryan@openingdesign.com | 773.425.6456

HERNAN RESIDENCE - 05.29.2018
453 MATTERHORN DR - VERONA WI 53593
FRAMING - ROOFING - (\$103)

1

2

3

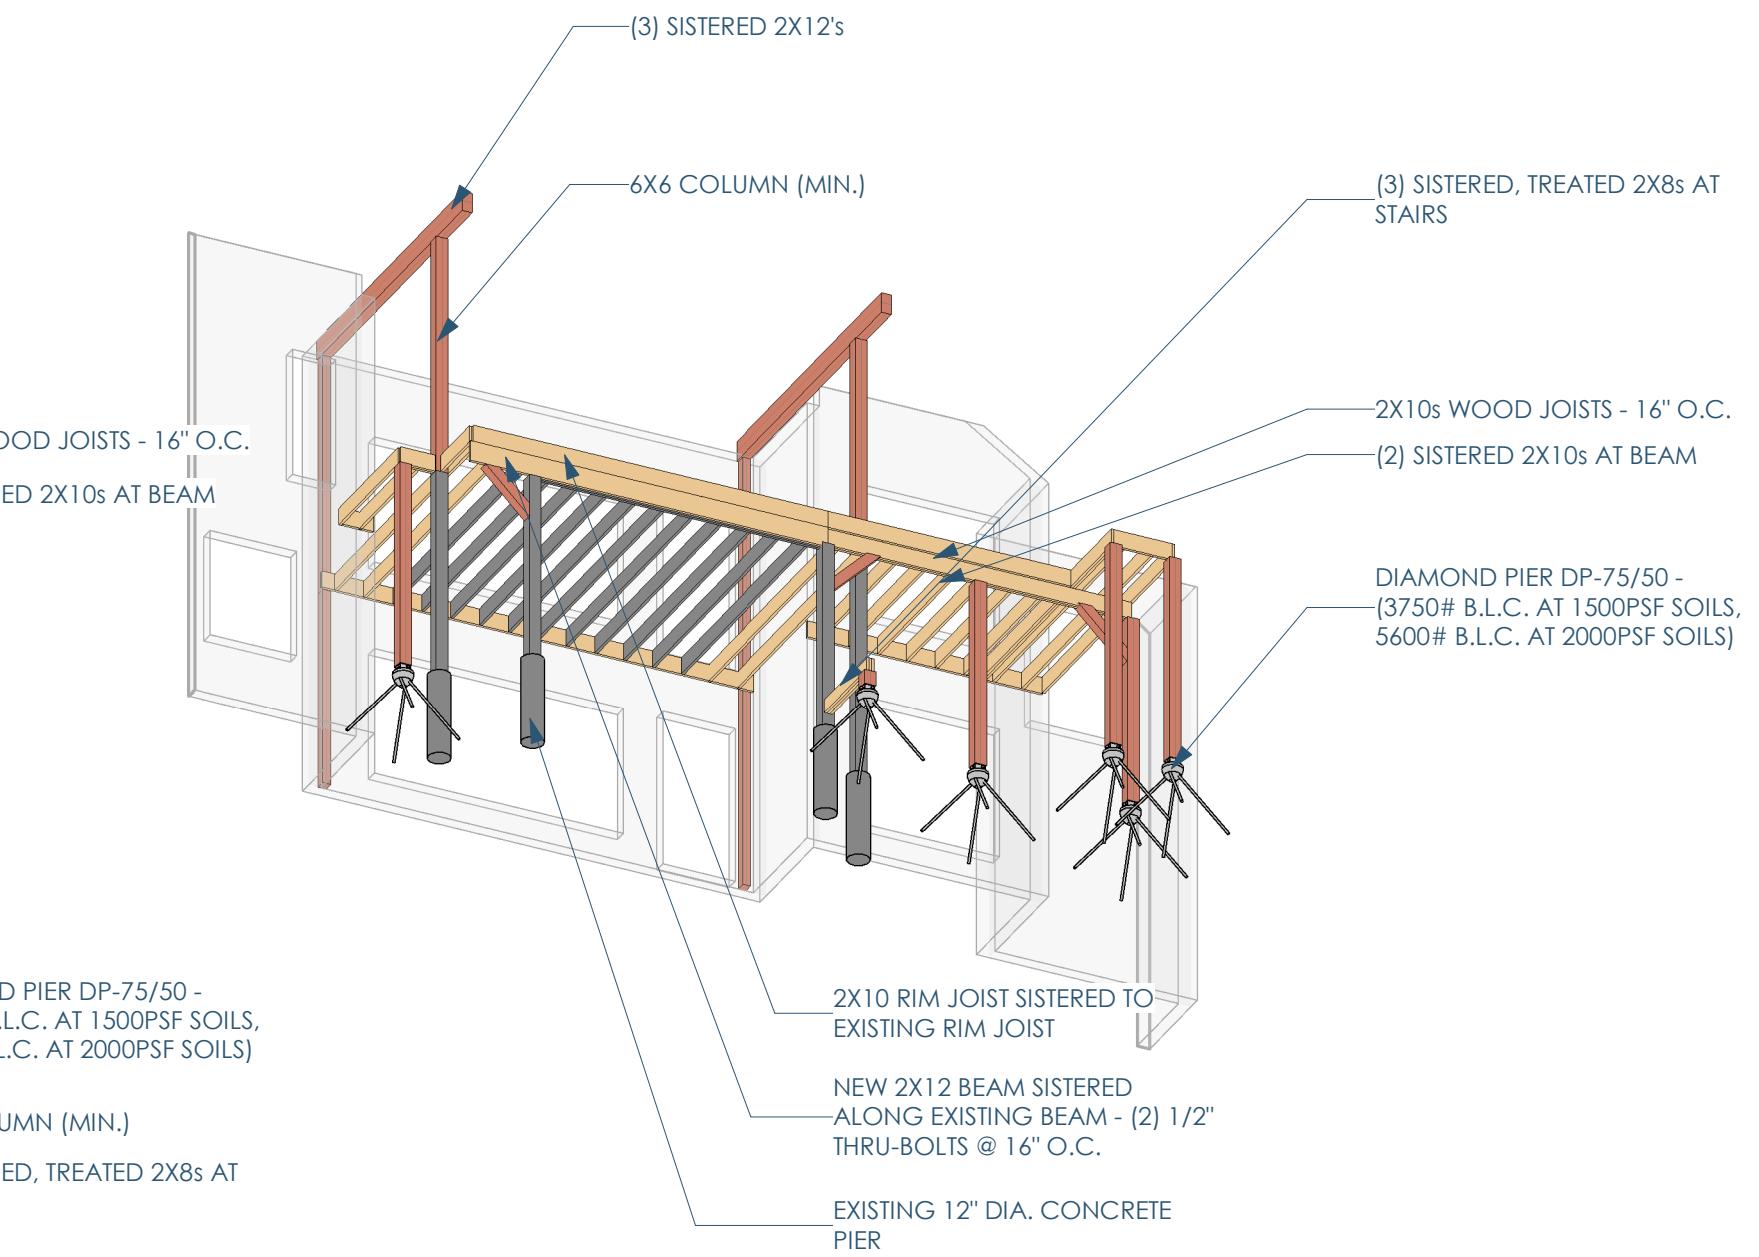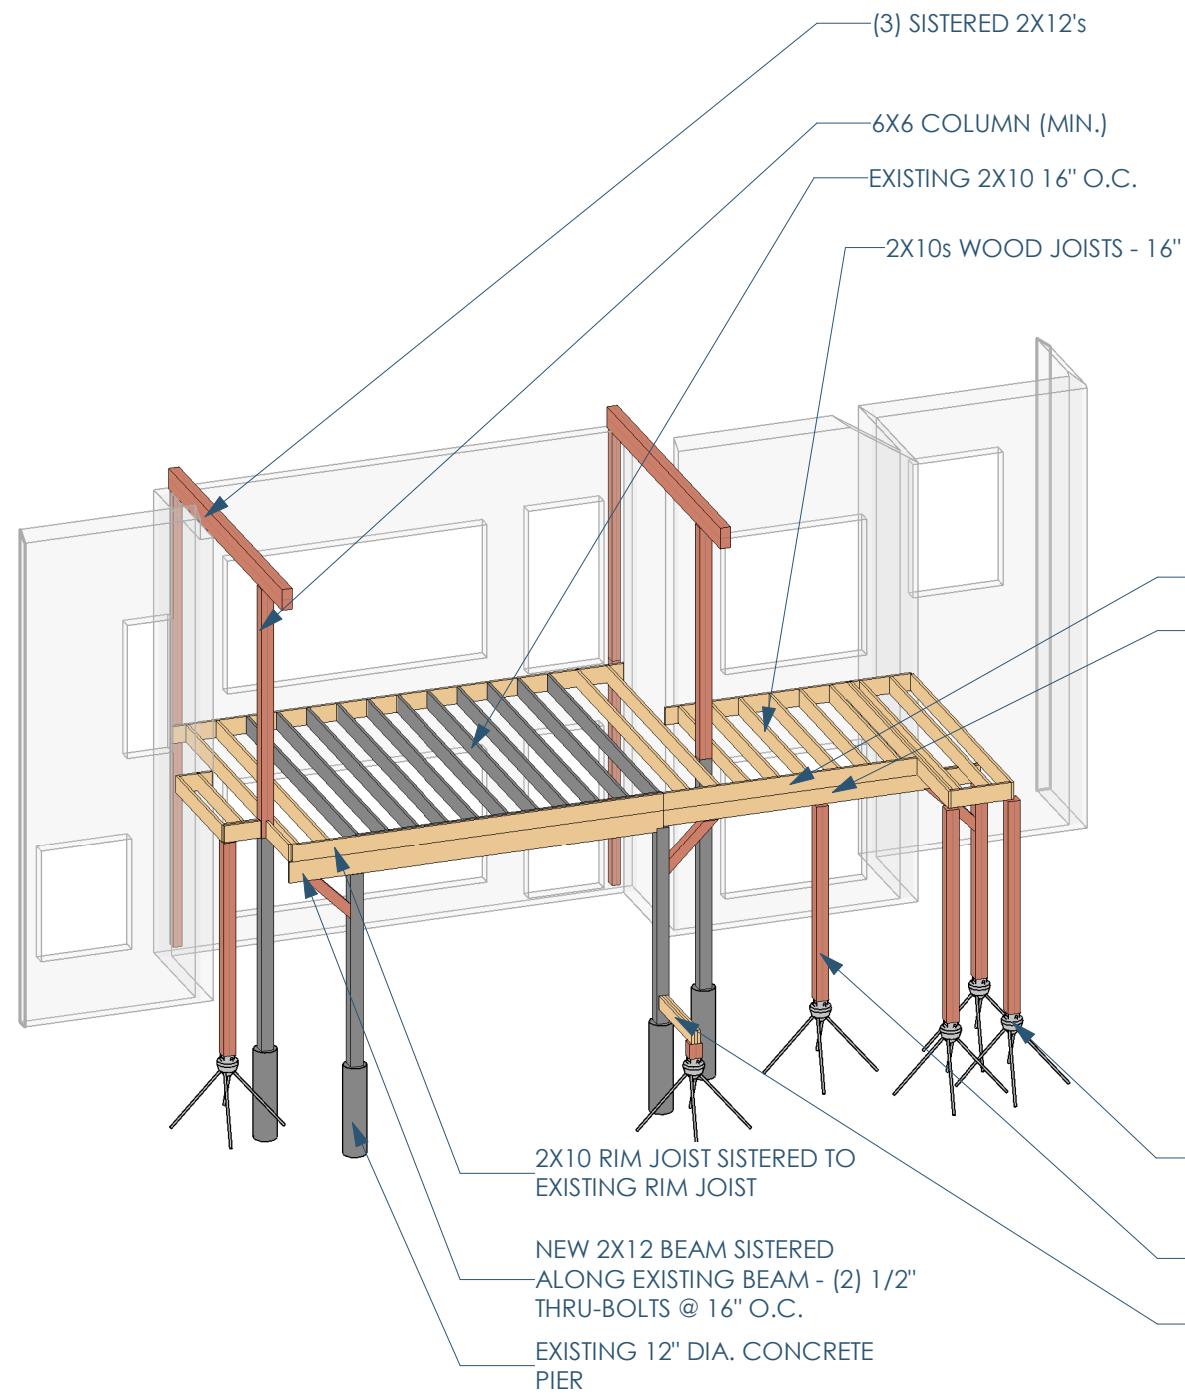

LAKE COUNTRY
CONSTRUCTION GROUP

General Contractor: Lake Country Construction Group
161 Horizon Dr. | Verona, WI 53593
608.845.1398



Architect: OpeningDesign
316 W Washington Ave. | Suite 675 | Madison, WI 53703
ryan@openingdesign.com | 773.425.6456

HERNAN RESIDENCE - 05.29.2018
453 MATTERHORN DR - VERONA WI 53593
FRAMING - 3D - (\$900)