


NEW COLUMN IN WALL
DOWN TO FOUNDATION

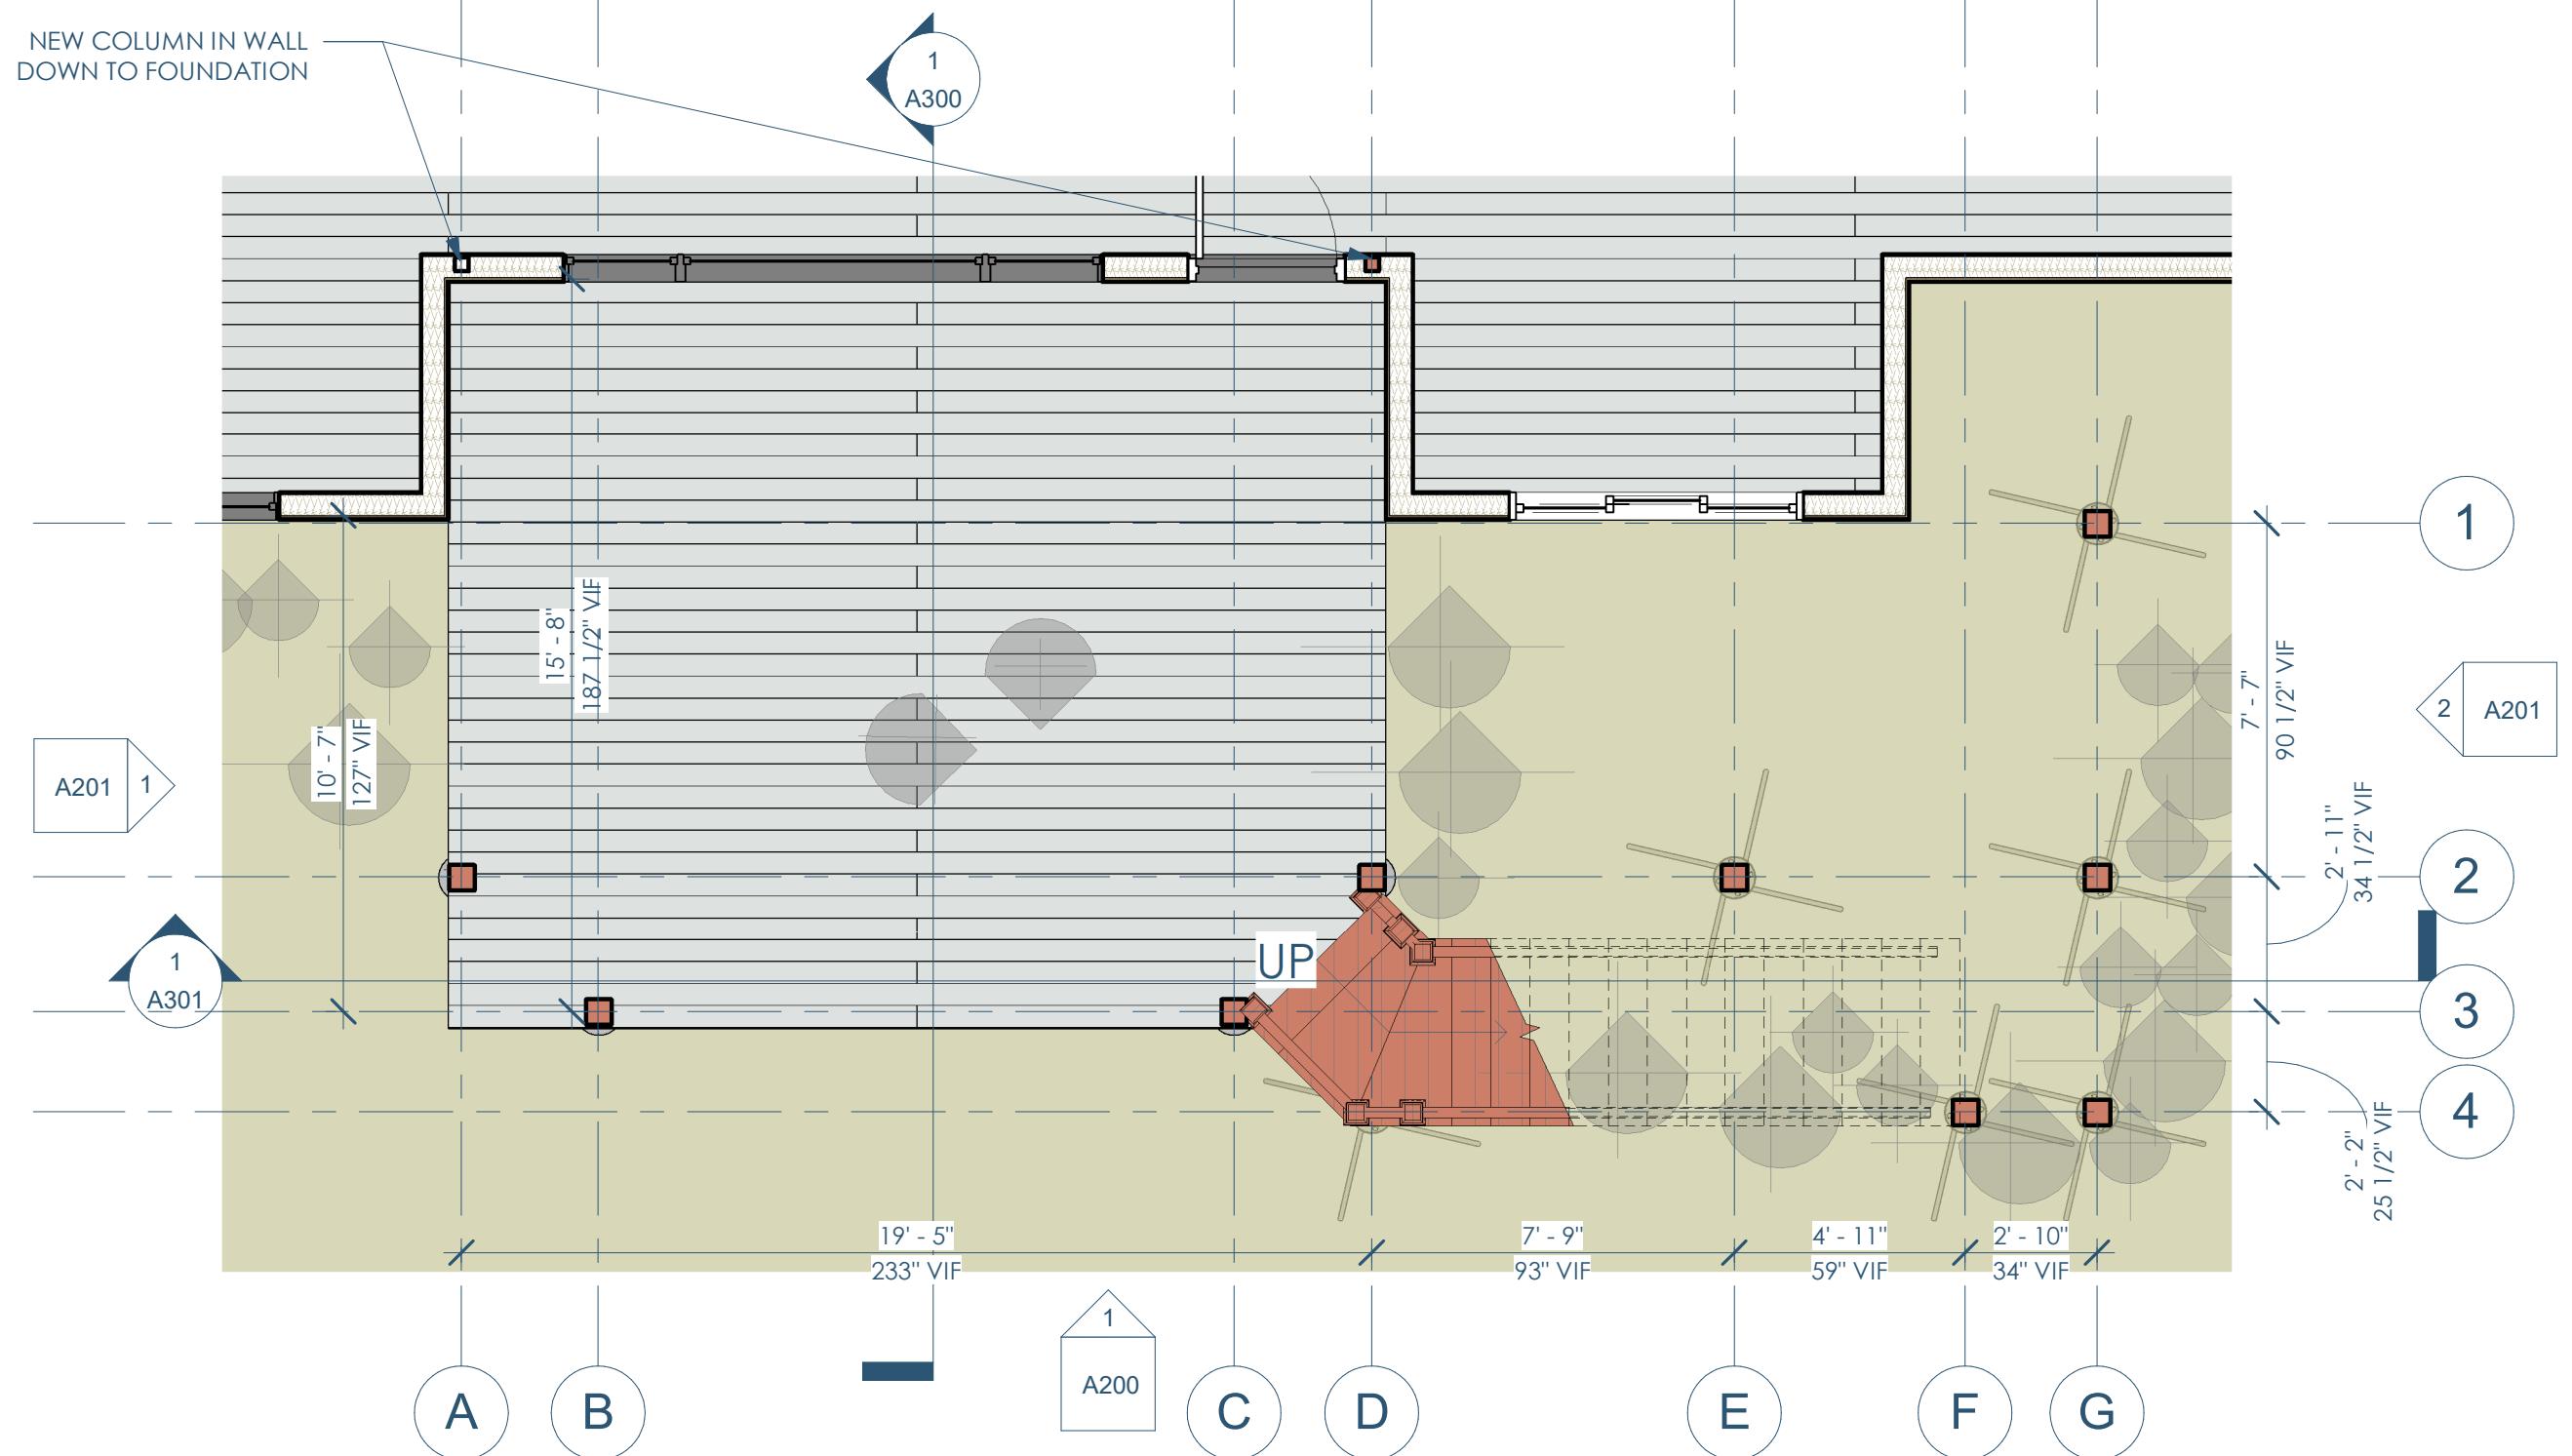

1A FLOOR PLAN - 1ST FLOOR
1/4" = 1'-0"

LAKE COUNTRY
CONSTRUCTION GROUP

General Contractor: Lake Country Construction Group
161 Horizon Dr. | Verona, WI 53593
608.845.1398




Architect: OpeningDesign

316 W Washington Ave. | Suite 675 | Madison, WI 53703
ryan@openingdesign.com | 773.425.6456

HERNAN RESIDENCE - 05.18.2018
453 MATTERHORN DR - VERONA WI 53593
FLOOR PLANS - 1ST FLOOR - (A100)



NEW COLUMN IN WALL
DOWN TO FOUNDATION

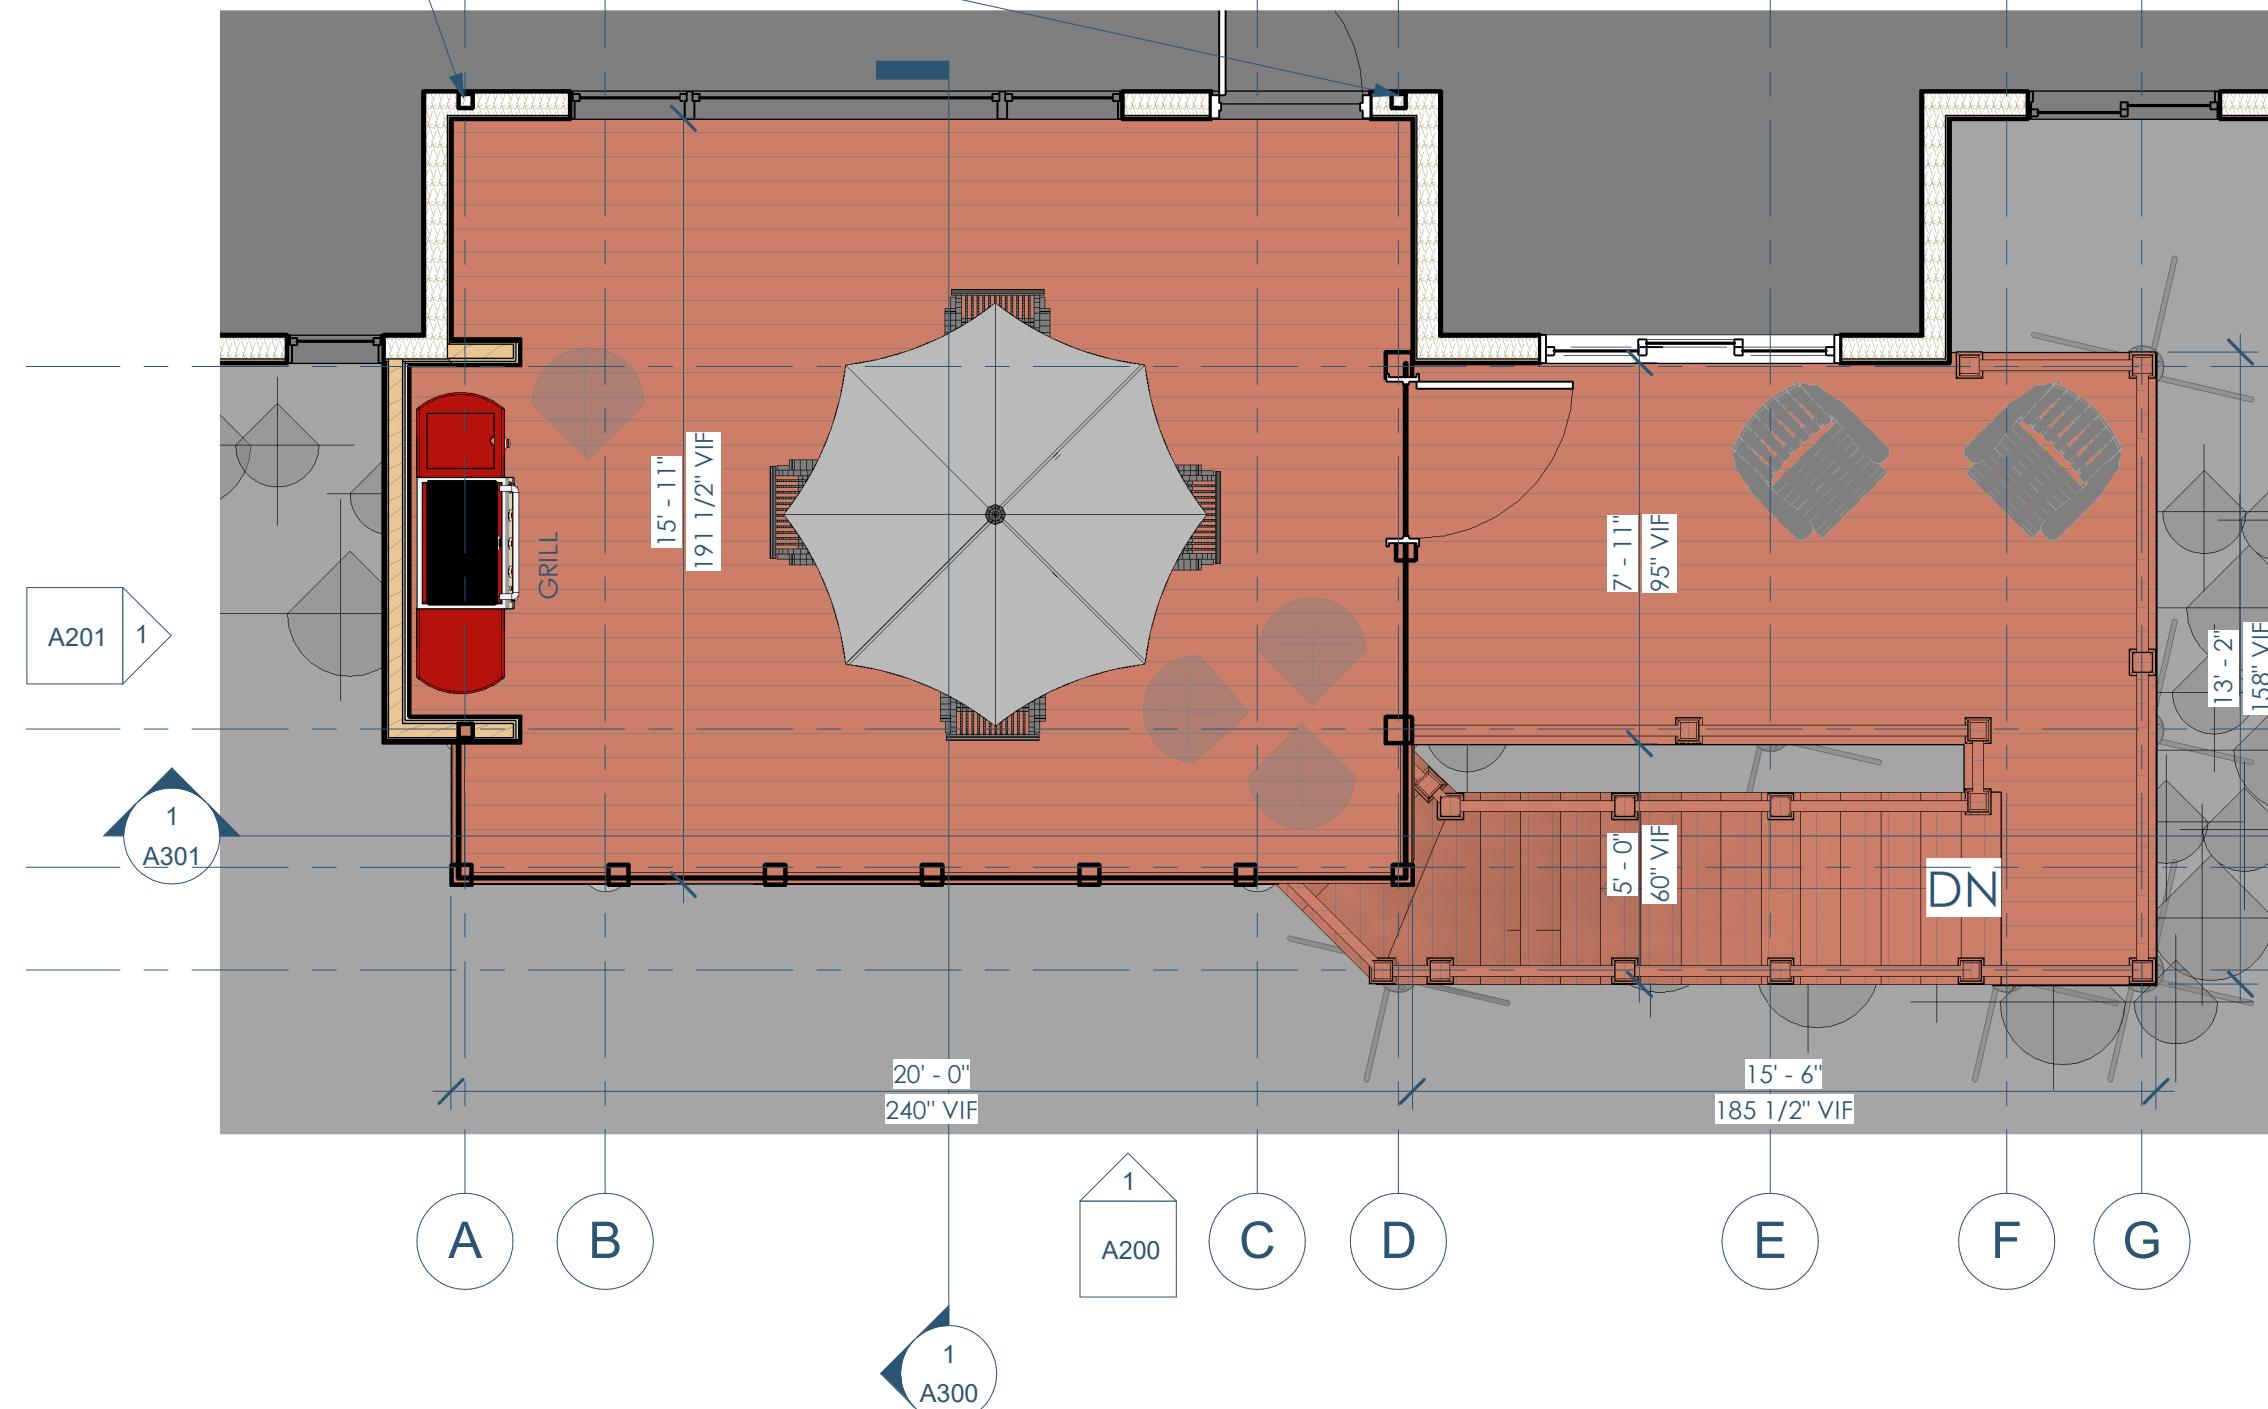

LAKE COUNTRY
CONSTRUCTION GROUP

General Contractor: Lake Country Construction Group
161 Horizon Dr. | Verona, WI 53593
608.845.1398




Architect: OpeningDesign

316 W Washington Ave. | Suite 675 | Madison, WI 53703
ryan@openingdesign.com | 773.425.6456

HERNAN RESIDENCE - 05.18.2018
453 MATTERHORN DR - VERONA WI 53593
FLOOR PLAN - 2ND FLOOR - (A102)



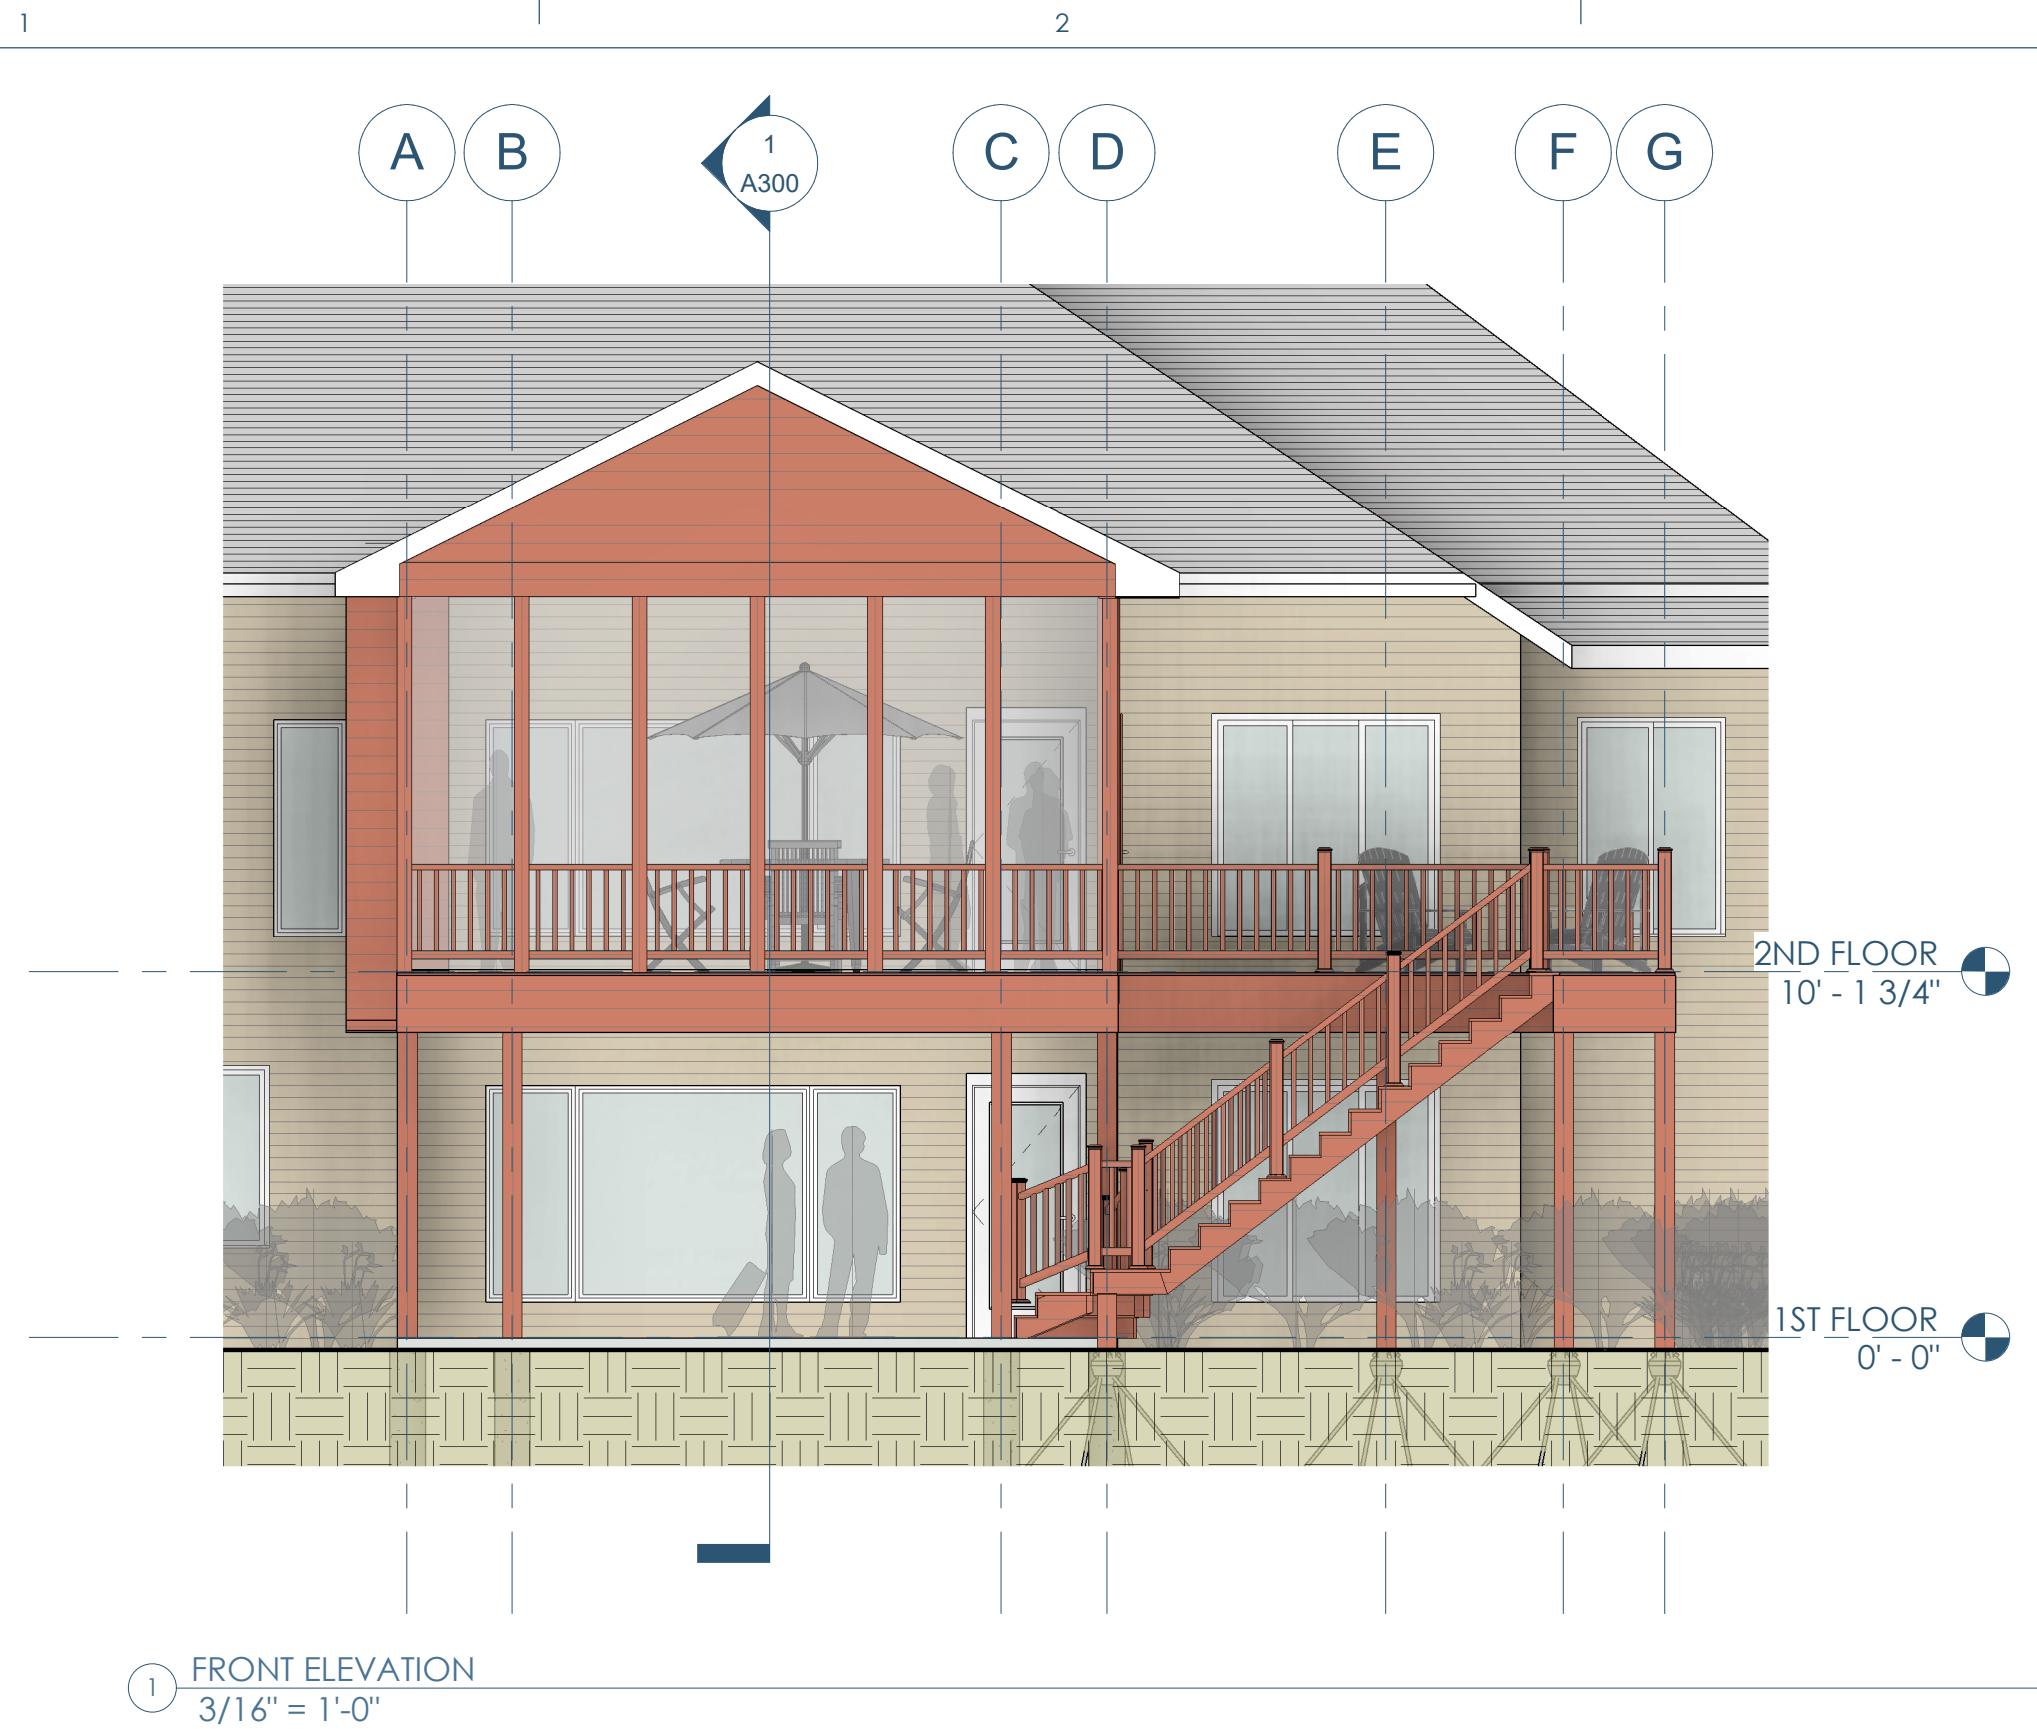

LAKE COUNTRY
CONSTRUCTION GROUP

General Contractor: Lake Country Construction Group
161 Horizon Dr. | Verona, WI 53593
608.845.1398



Architect: OpeningDesign

316 W Washington Ave. | Suite 675 | Madison, WI 53703
ryan@openingdesign.com | 773.425.6456



HERNAN RESIDENCE - 05.18.2018
453 MATTERHORN DR - VERONA, WI 53593
BUILDING ELEVATIONS - (A200)



1 2 3

2

3

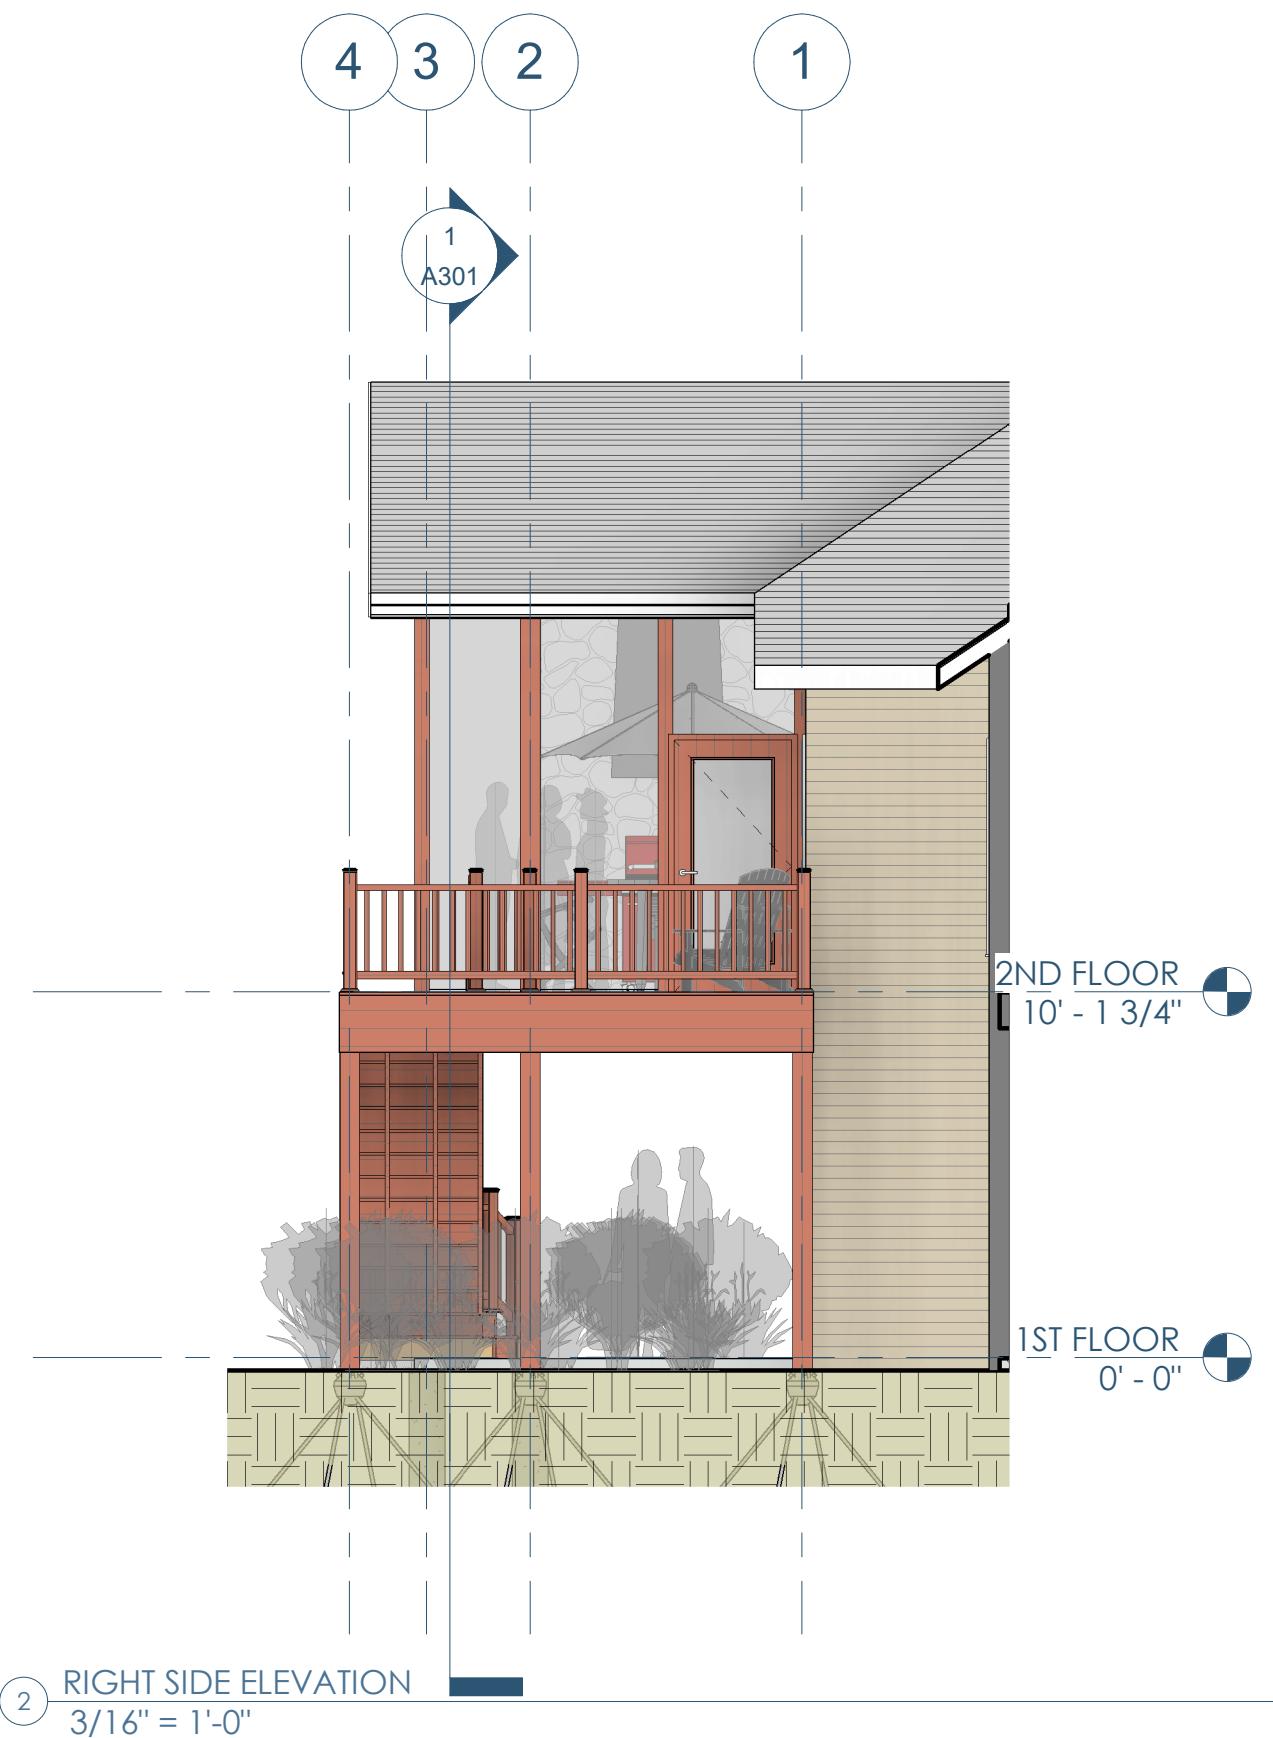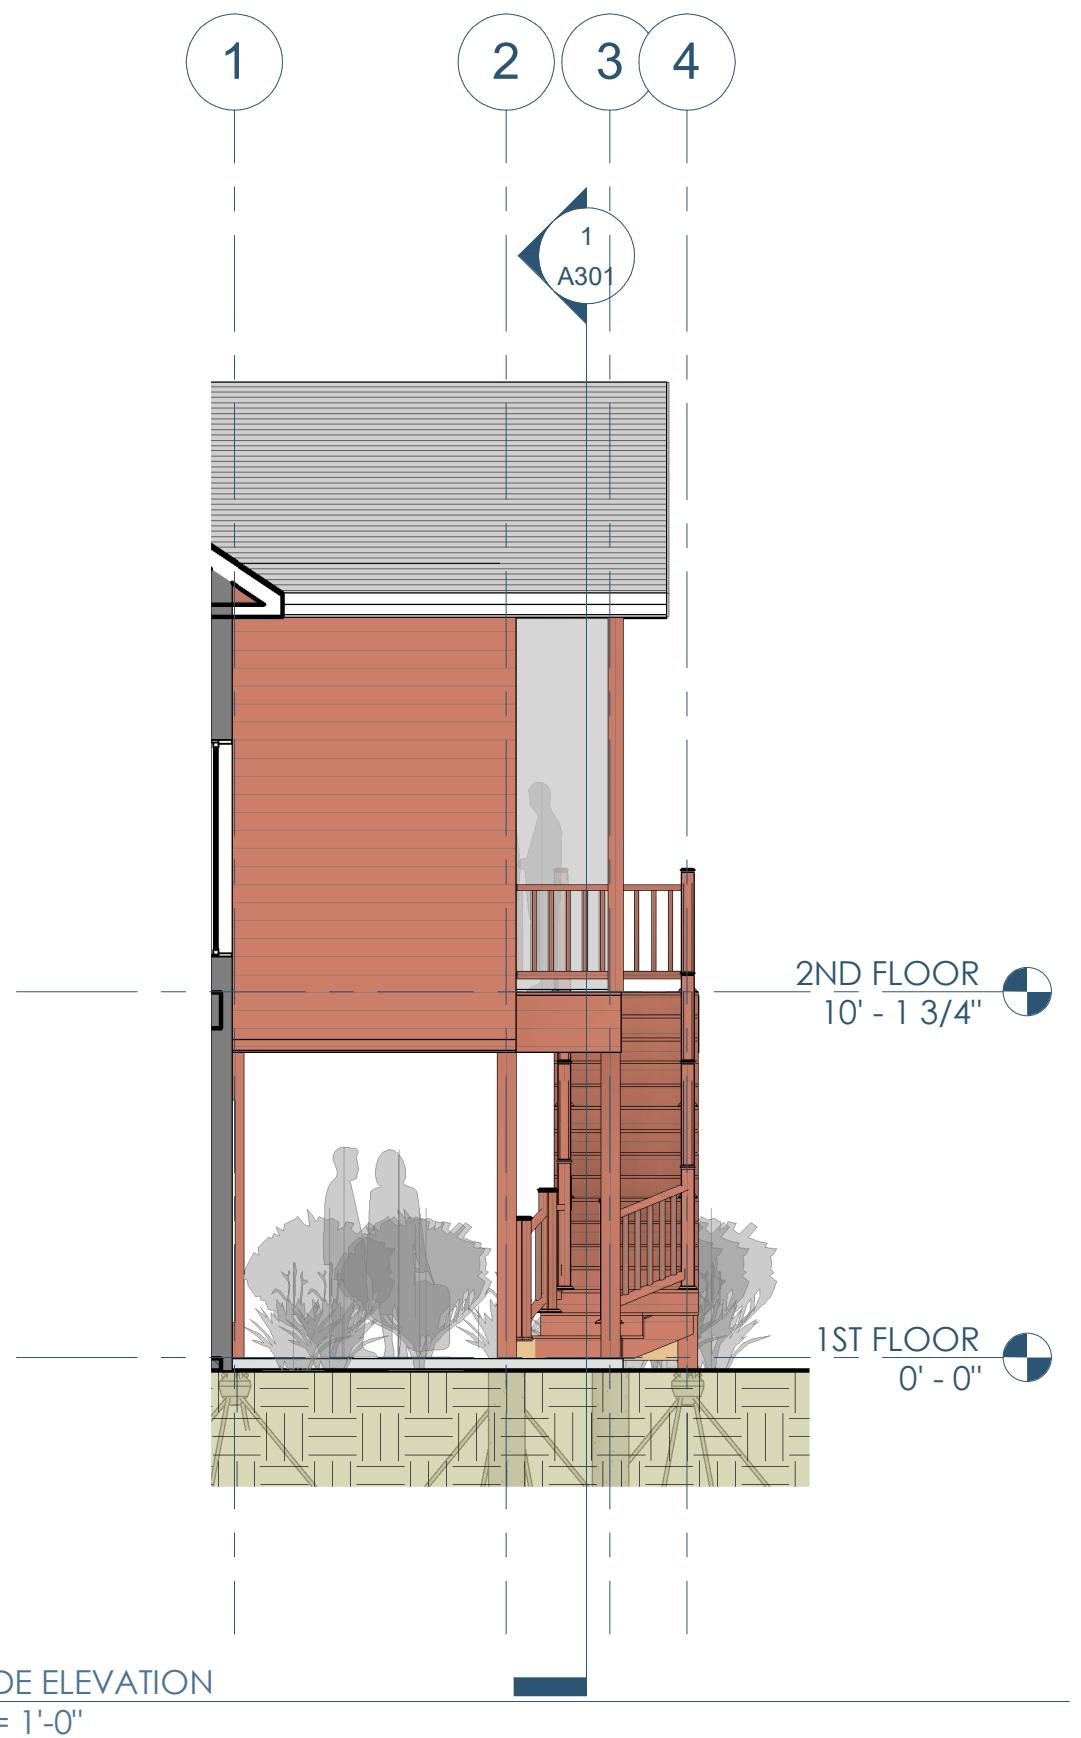

LAKE COUNTRY
CONSTRUCTION GROUP

General Contractor: Lake Country Construction Group
161 Horizon Dr. | Verona, WI 53593
608.845.1398



Architect: OpeningDesign

316 W Washington Ave | Suite 675 | Madison, WI 53703
ryan@openingadesign.com | 773.425.6456

HERNAN RESIDENCE - 05.18.2018
453 MATTERHORN DR - VERONA WI 53593
BUILDING ELEVATIONS - (A201)

1 2 3

C


C

B

B

A

A

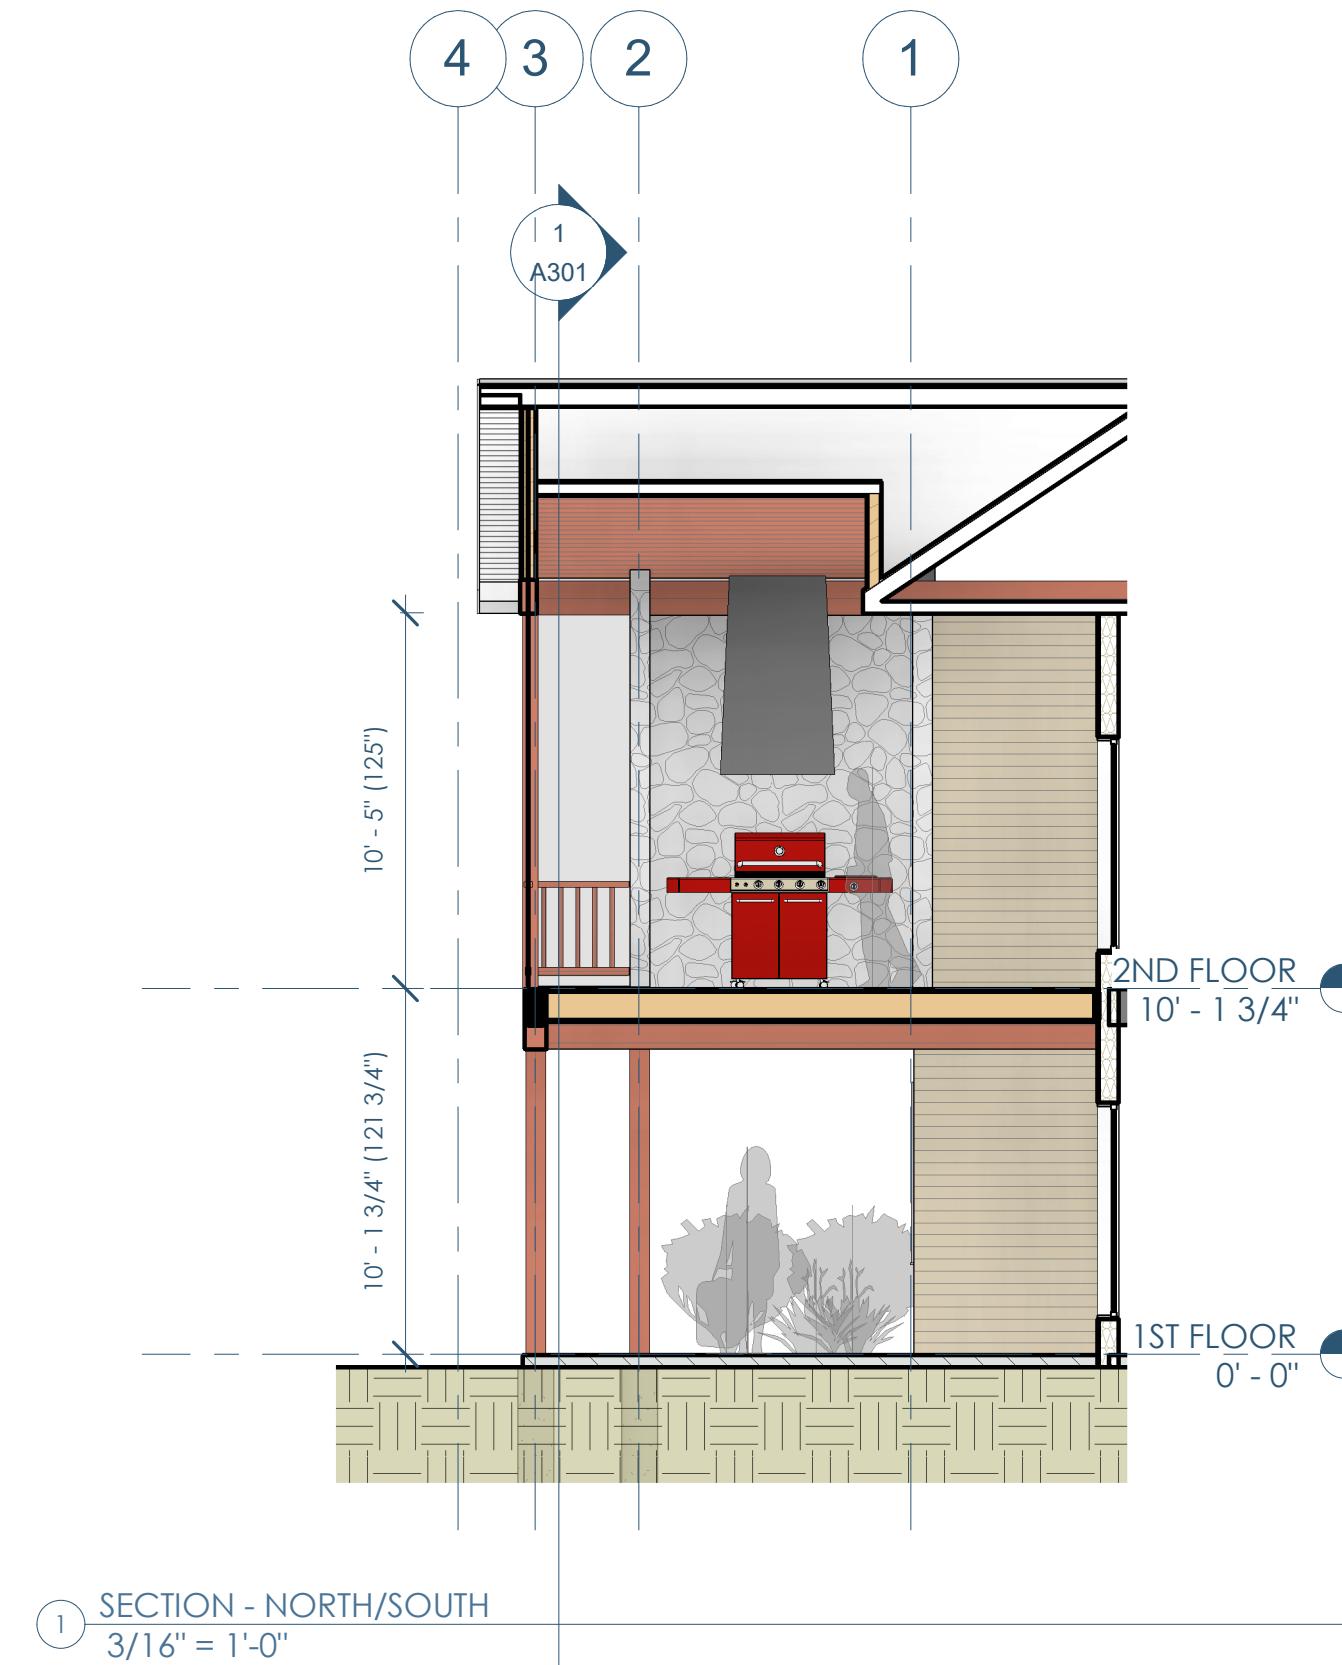

LAKE COUNTRY
CONSTRUCTION GROUP

General Contractor: Lake Country Construction Group
161 Horizon Dr. | Verona, WI 53593
608.845.1398



Architect: OpeningDesign

316 W Washington Ave. | Suite 675 | Madison, WI 53703
ryan@openingdesign.com | 773.425.6456

HERNAN RESIDENCE - 05.18.2018
453 MATTERHORN DR - VERONA, WI 53593
BUILDING SECTIONS - (A300)

1 2 3

LAKE COUNTRY

CONSTRUCTION GROUP

General Contractor: Lake Country Construction Group
161 Horizon Dr. | Verona, WI 53593
608.845.1398



Architect: OpeningDesign

316 W Washington Ave. | Suite 675 | Madison, WI 53703
ryan@openingdesign.com | 773.425.6456

HERNAN RESIDENCE - 05.18.2018
453 MATTERHORN DR - VERONA WI 53593
BUILDING SECTION - (A301)

① SECTION - EAST/WEST
 $3/16'' = 1'-0''$

1


2

3

1

2

3

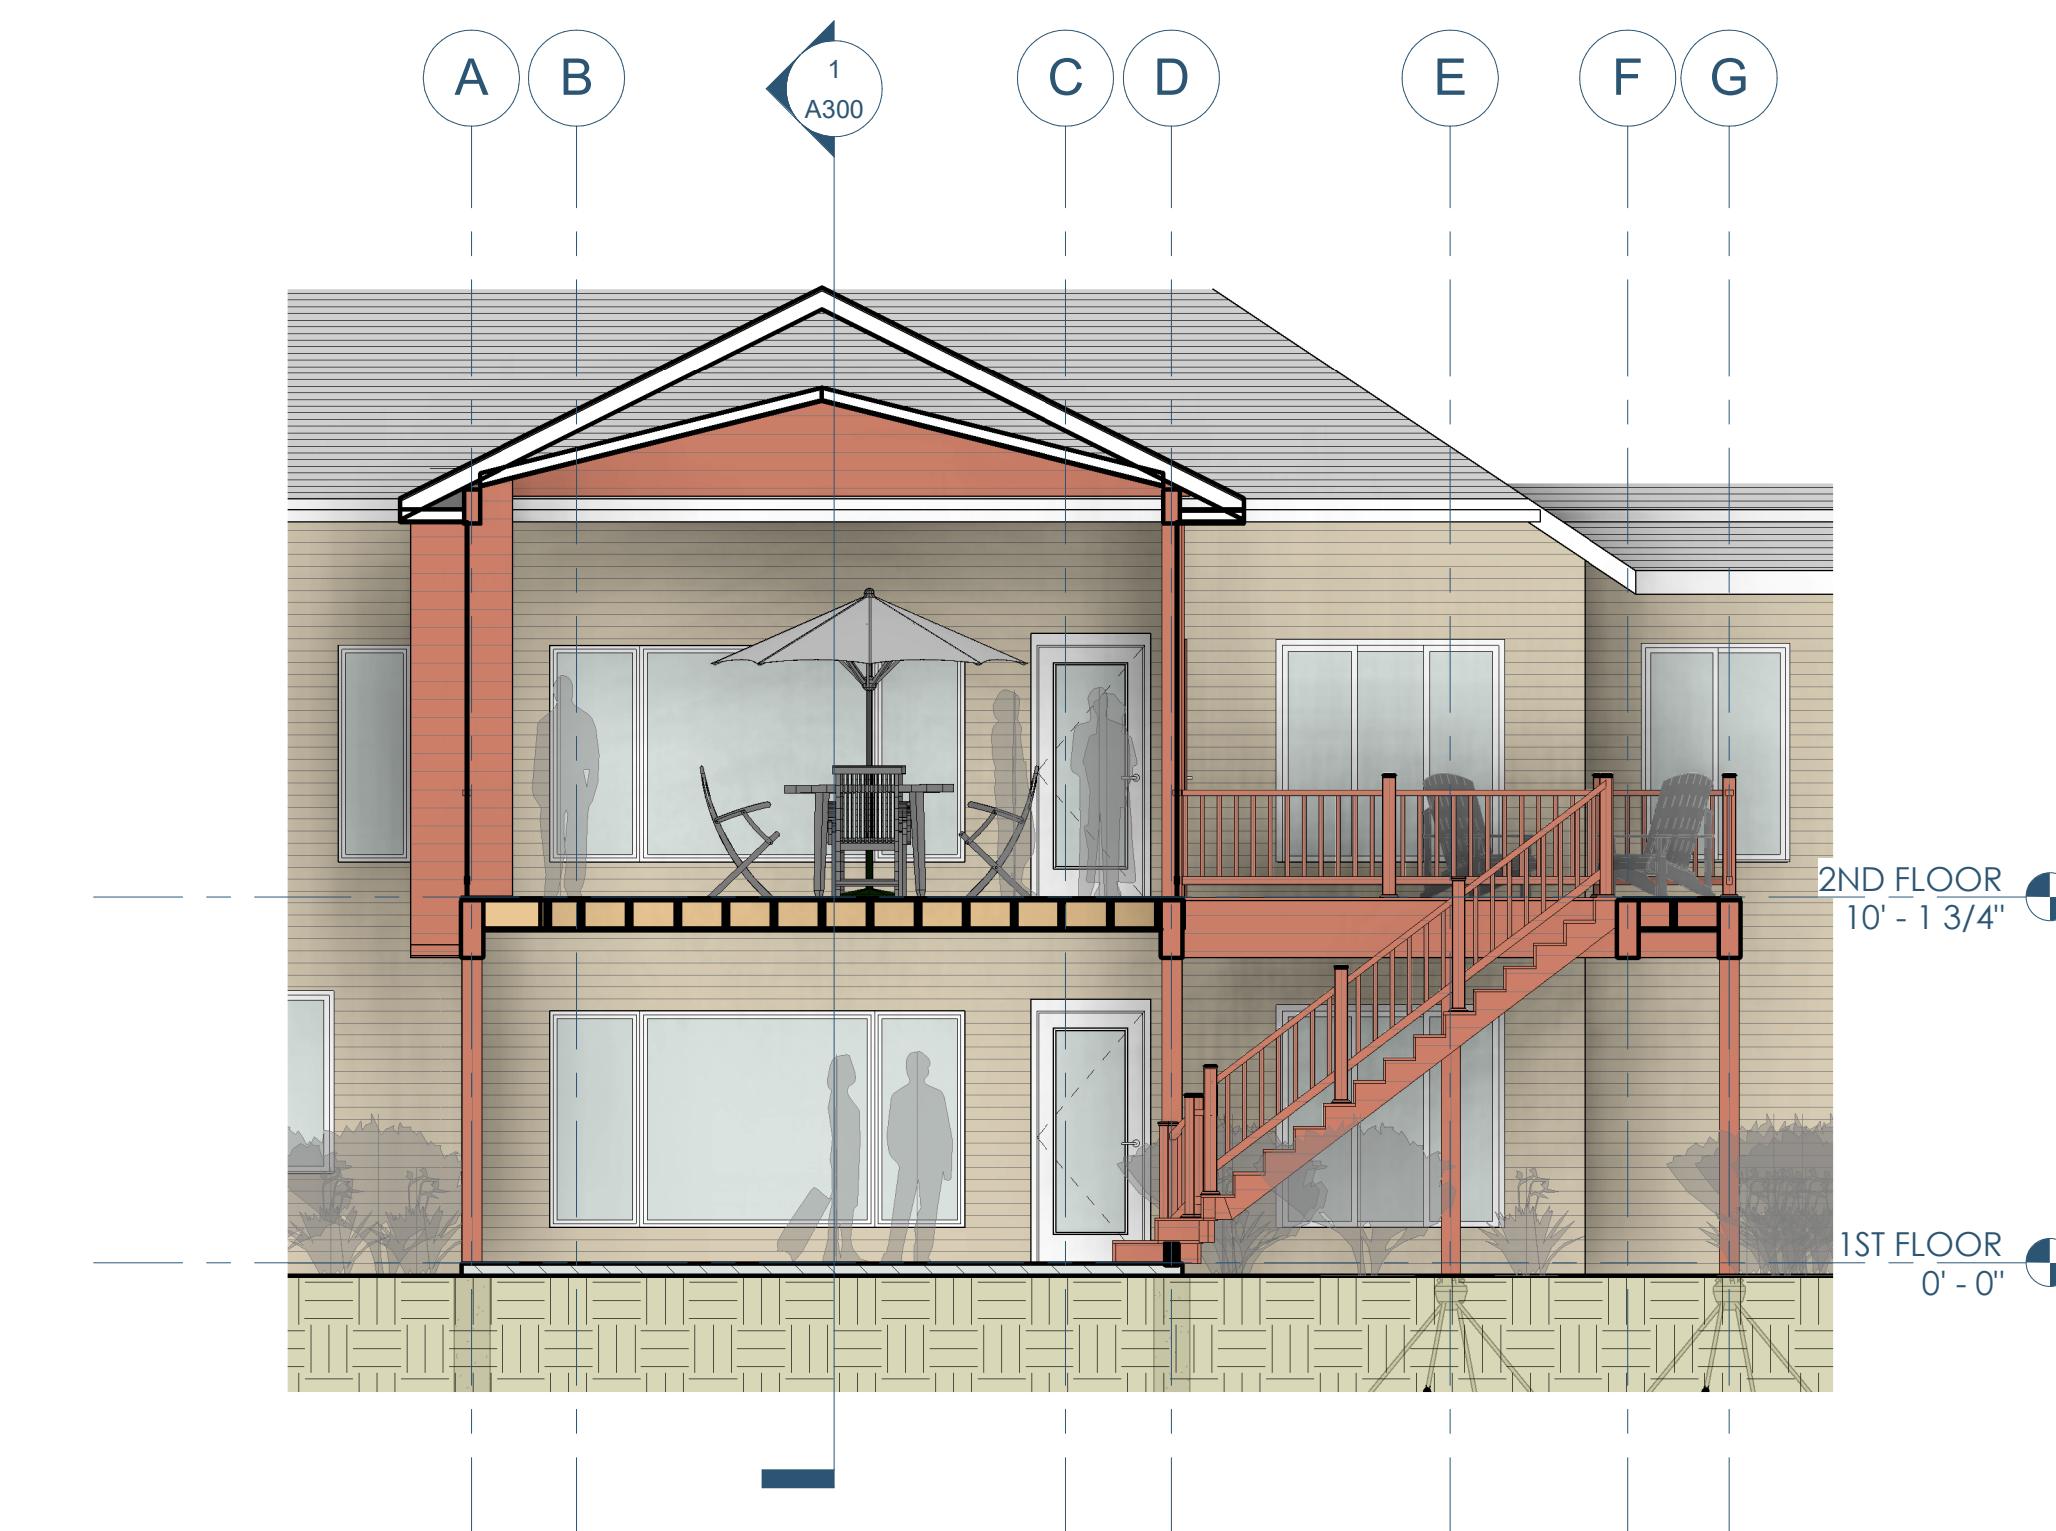



① PERSPECTIVE 1



② PERSPECTIVE 2


**LAKE COUNTRY
CONSTRUCTION GROUP**

General Contractor: Lake Country Construction Group
161 Horizon Dr. | Verona, WI 53593
608.845.1398



Architect: OpeningDesign
316 W Washington Ave. | Suite 675 | Madison, WI 53703
ryan@openingdesign.com | 773.425.6456

HERNAN RESIDENCE - 05.18.2018
453 MATTERHORN DR - VERONA, WI 53593
3D VIEWS - (A900)

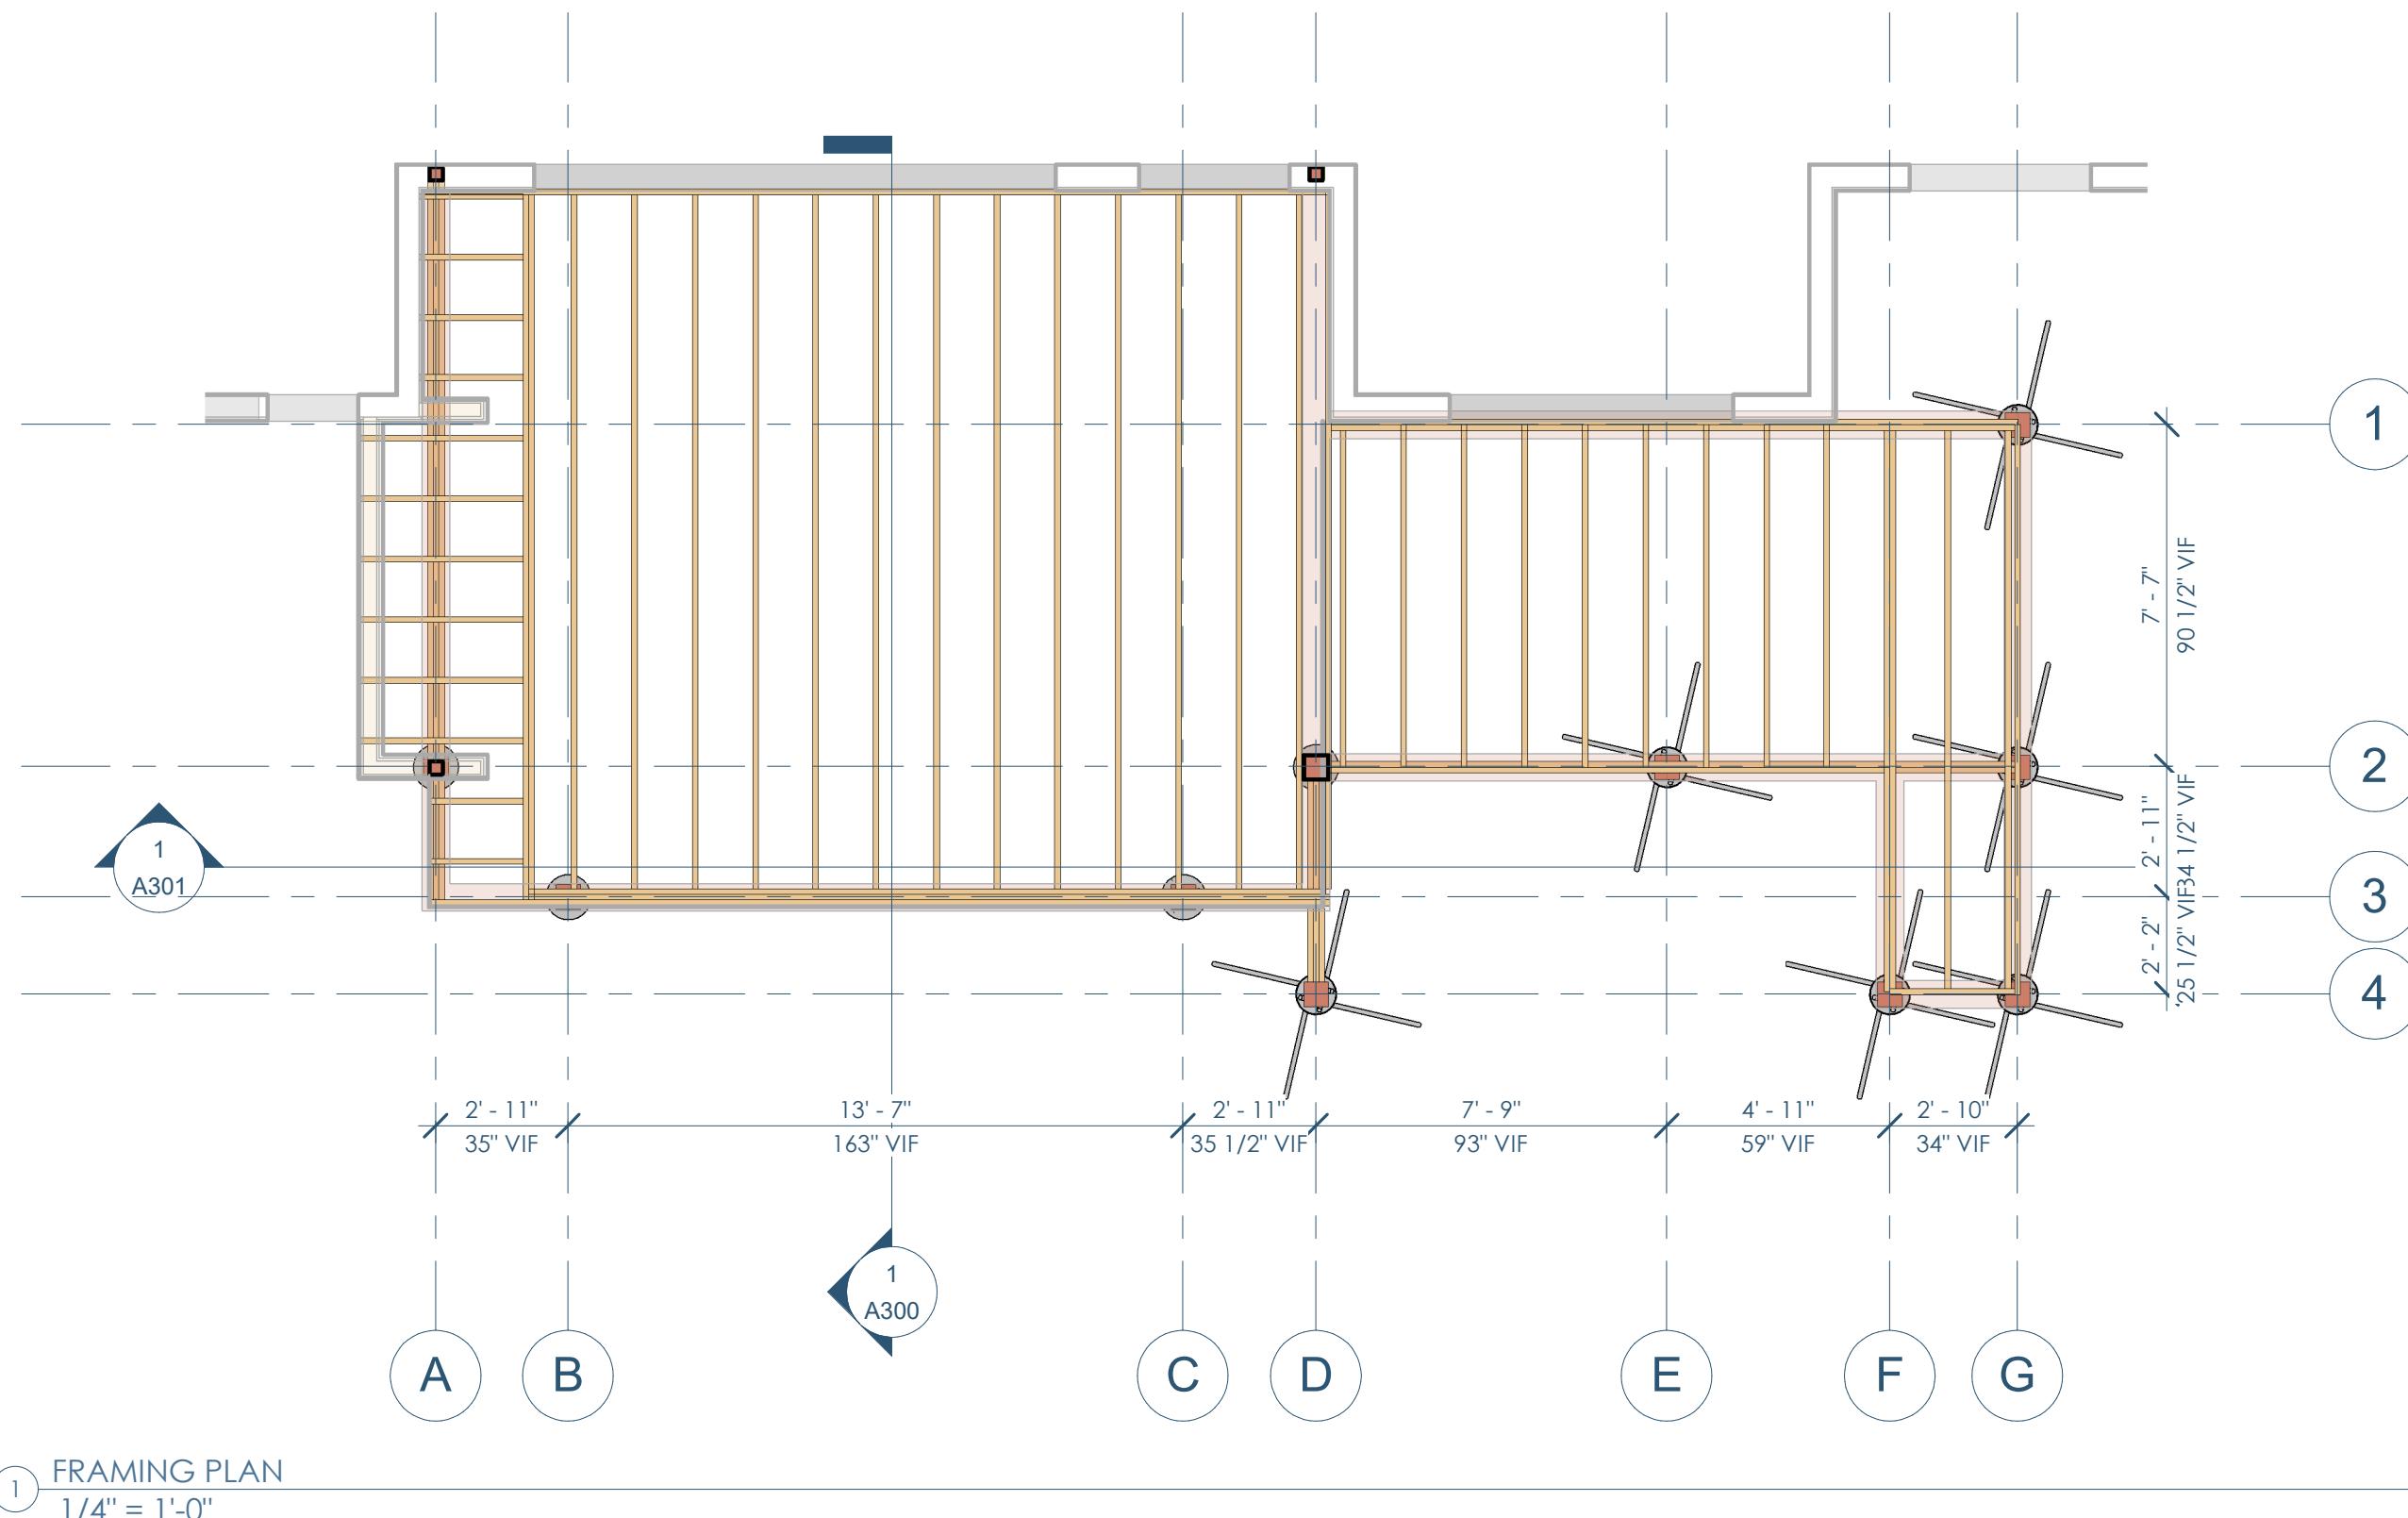

LAKE COUNTRY
CONSTRUCTION GROUP




General Contractor: Lake Country Construction Group
161 Horizon Dr. | Verona, WI 53593
608.845.1398


Architect: OpeningDesign

316 W Washington Ave. | Suite 675 | Madison, WI 53703
ryan@openingdesign.com | 773.425.6456

HERNAN RESIDENCE - 05.18.2018
453 MATTERHORN DR - VERONA WI 53593
FRAMING - (\$102)

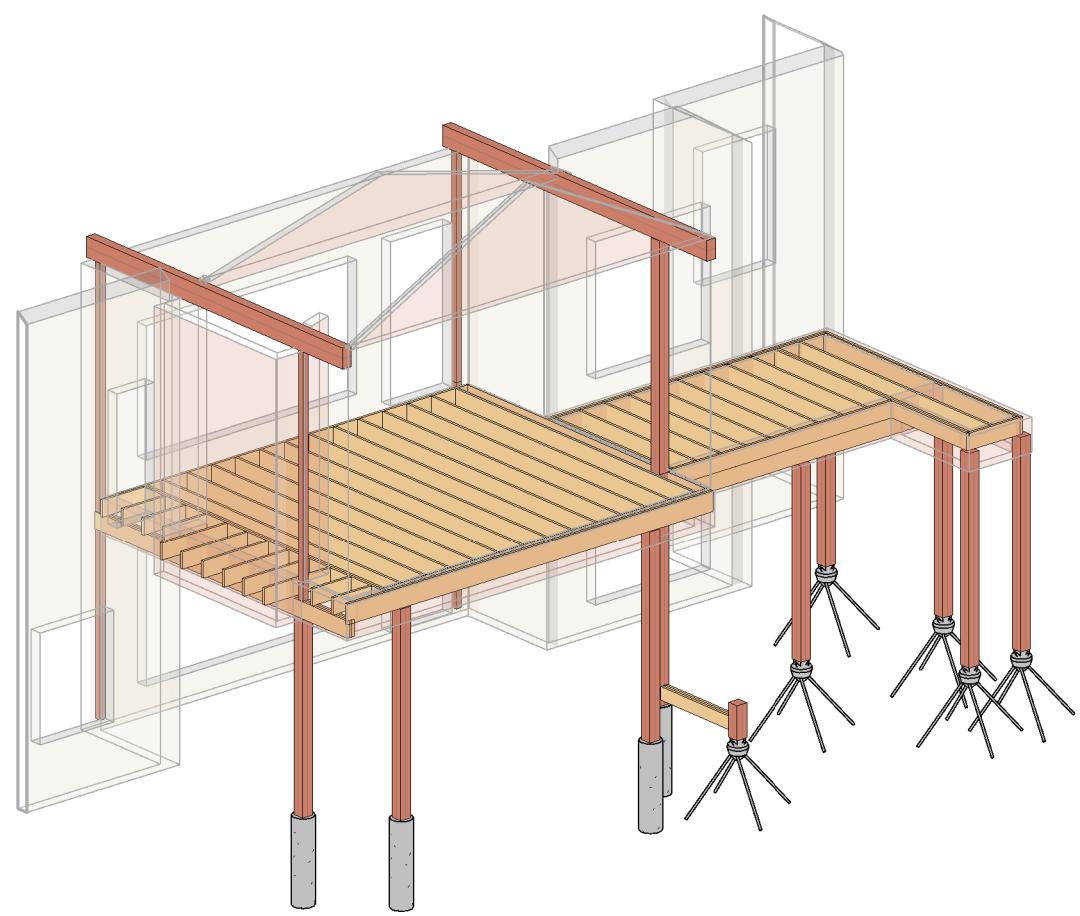

1 STRUCTURE - VIEW 1

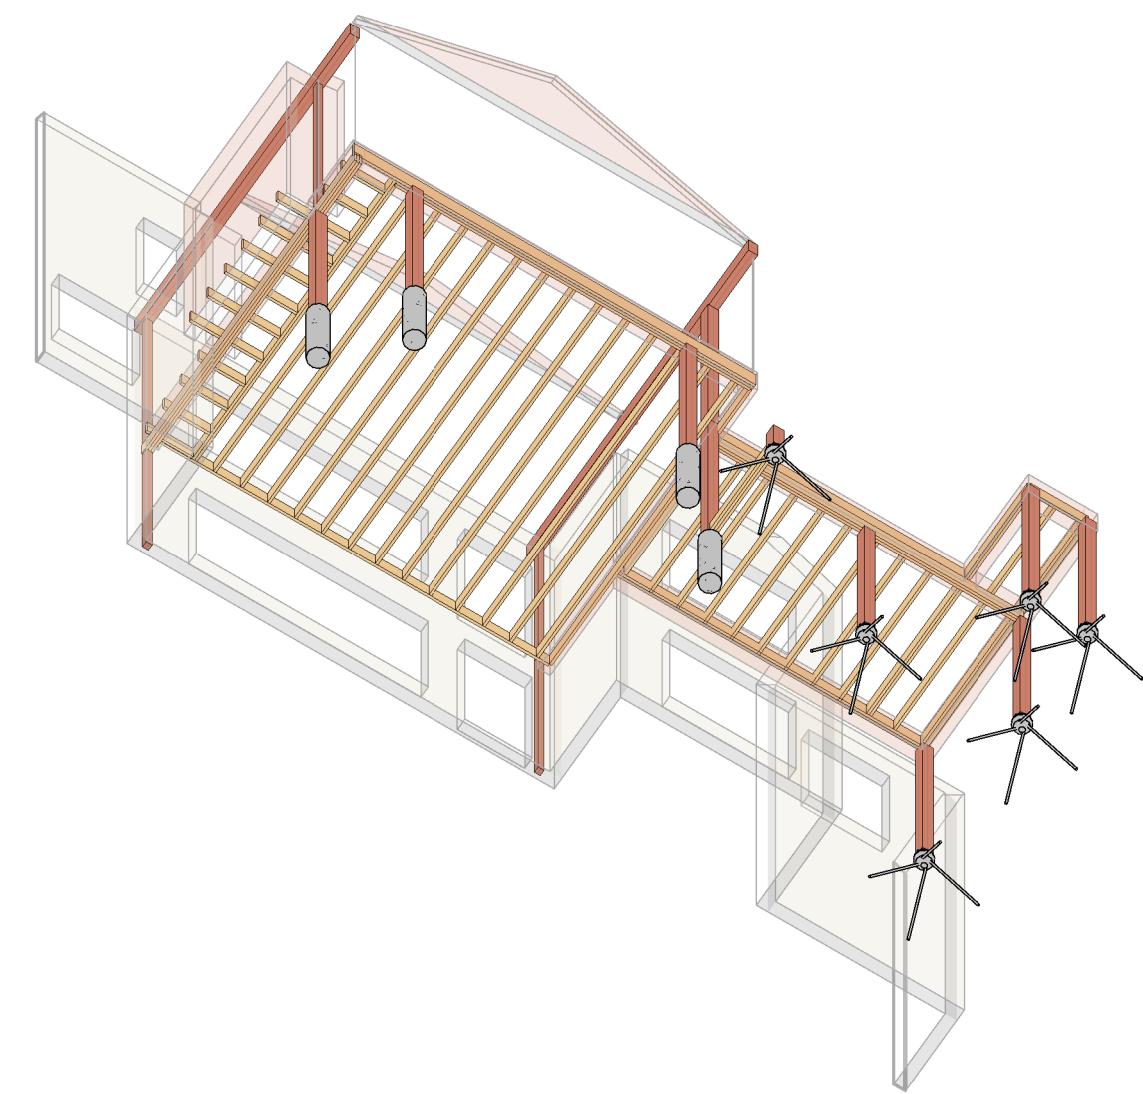

2 STRUCTURE - VIEW 2

LAKE COUNTRY
CONSTRUCTION GROUP

General Contractor: Lake Country Construction Group
161 Horizon Dr. | Verona, WI 53593
608.845.1398



Architect: OpeningDesign
316 W Washington Ave. | Suite 675 | Madison, WI 53703
ryan@openingdesign.com | 773.425.6456

HERNAN RESIDENCE - 05.18.2018
453 MATTERHORN DR - VERONA WI 53593
FRAMING - 3D - (\$900)